


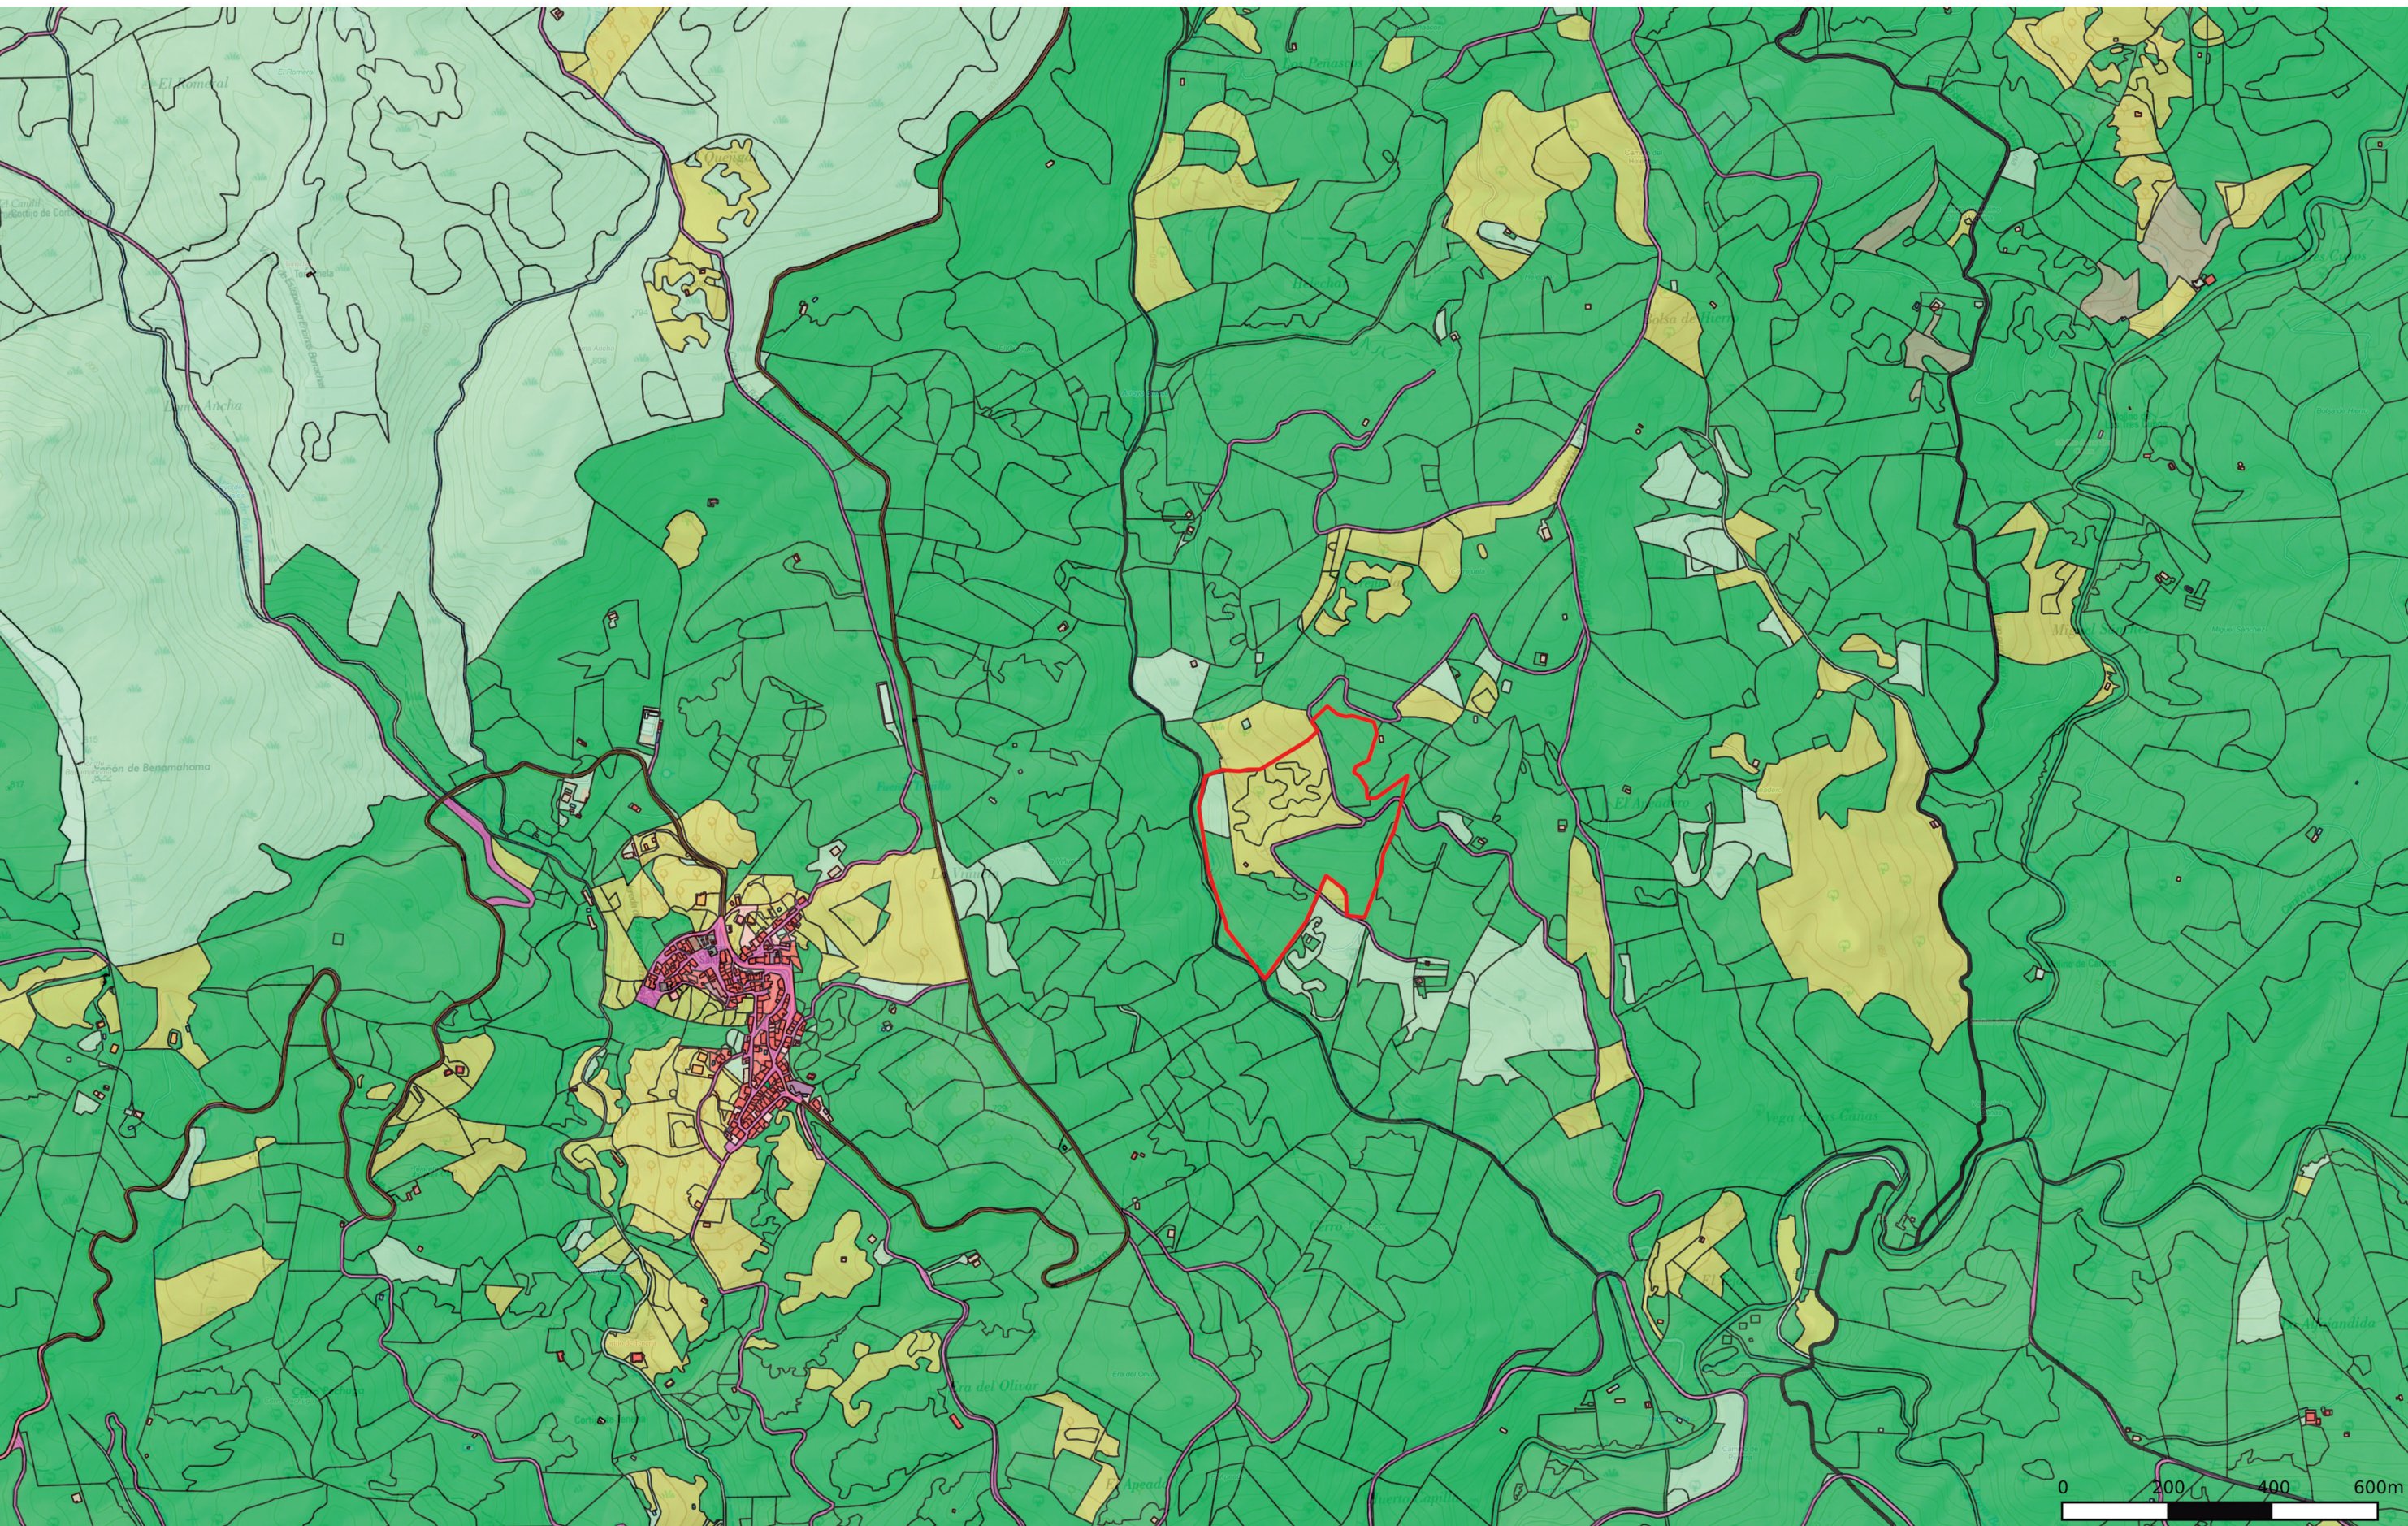

● USO AGRÍCOLA ● USO FORESTAL ● USO FORESTAL + OTRA ACTIVIDAD ECONÓMICA




● OLIVAR ● FRUTALES NO CÍTRICOS ● CUBIERTA FORESTAL

PLANO: CUBIERTA VEGETAL


PROYECTO DE ACTUACIÓN CENTRO ECO-TURISMO EN VIÑA DE JUAREZ, TÉRMINO MUNICIPAL DE CARTAJIMA - MÁLAGA

arquitecto: Rafael Segundo Navarro_colaborador: Miguel Orozco Martín

fecha: 12 de Septiembre de 2025

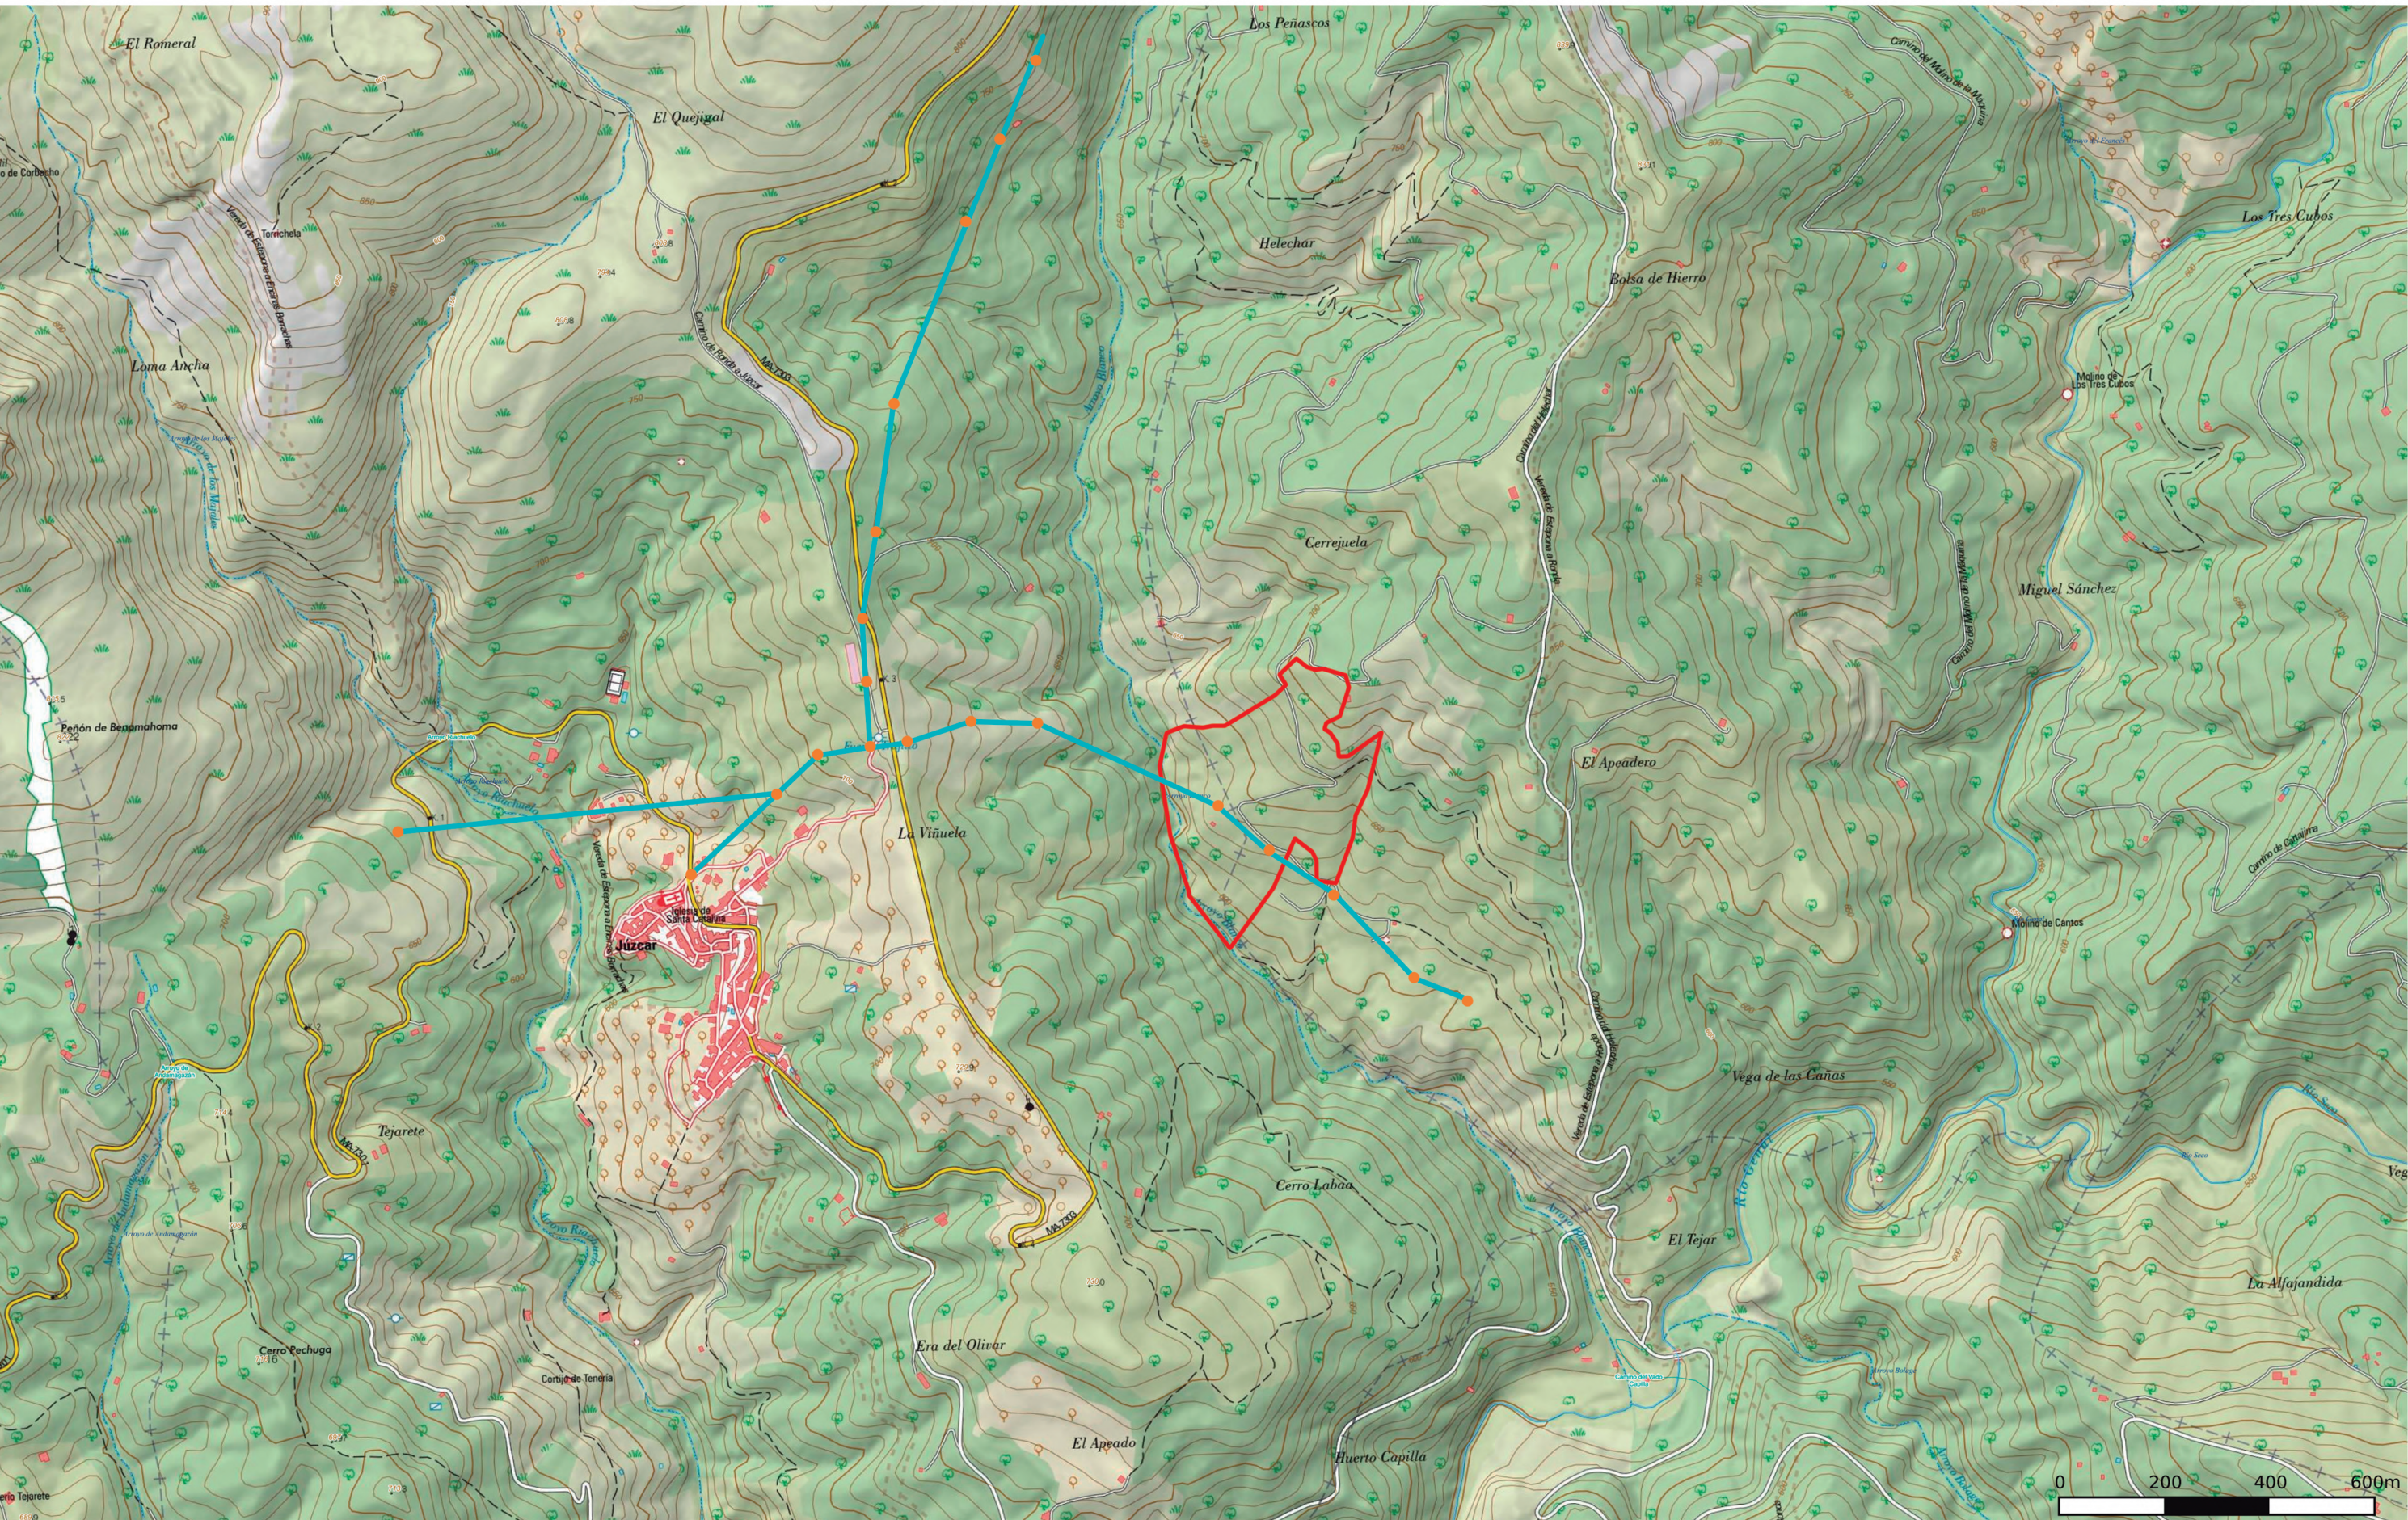

— LÍNEA DE MEDIA TENSIÓN (ÚNICA INFRAESTRUCTURA RELEVANTE EN LA PARCELA)

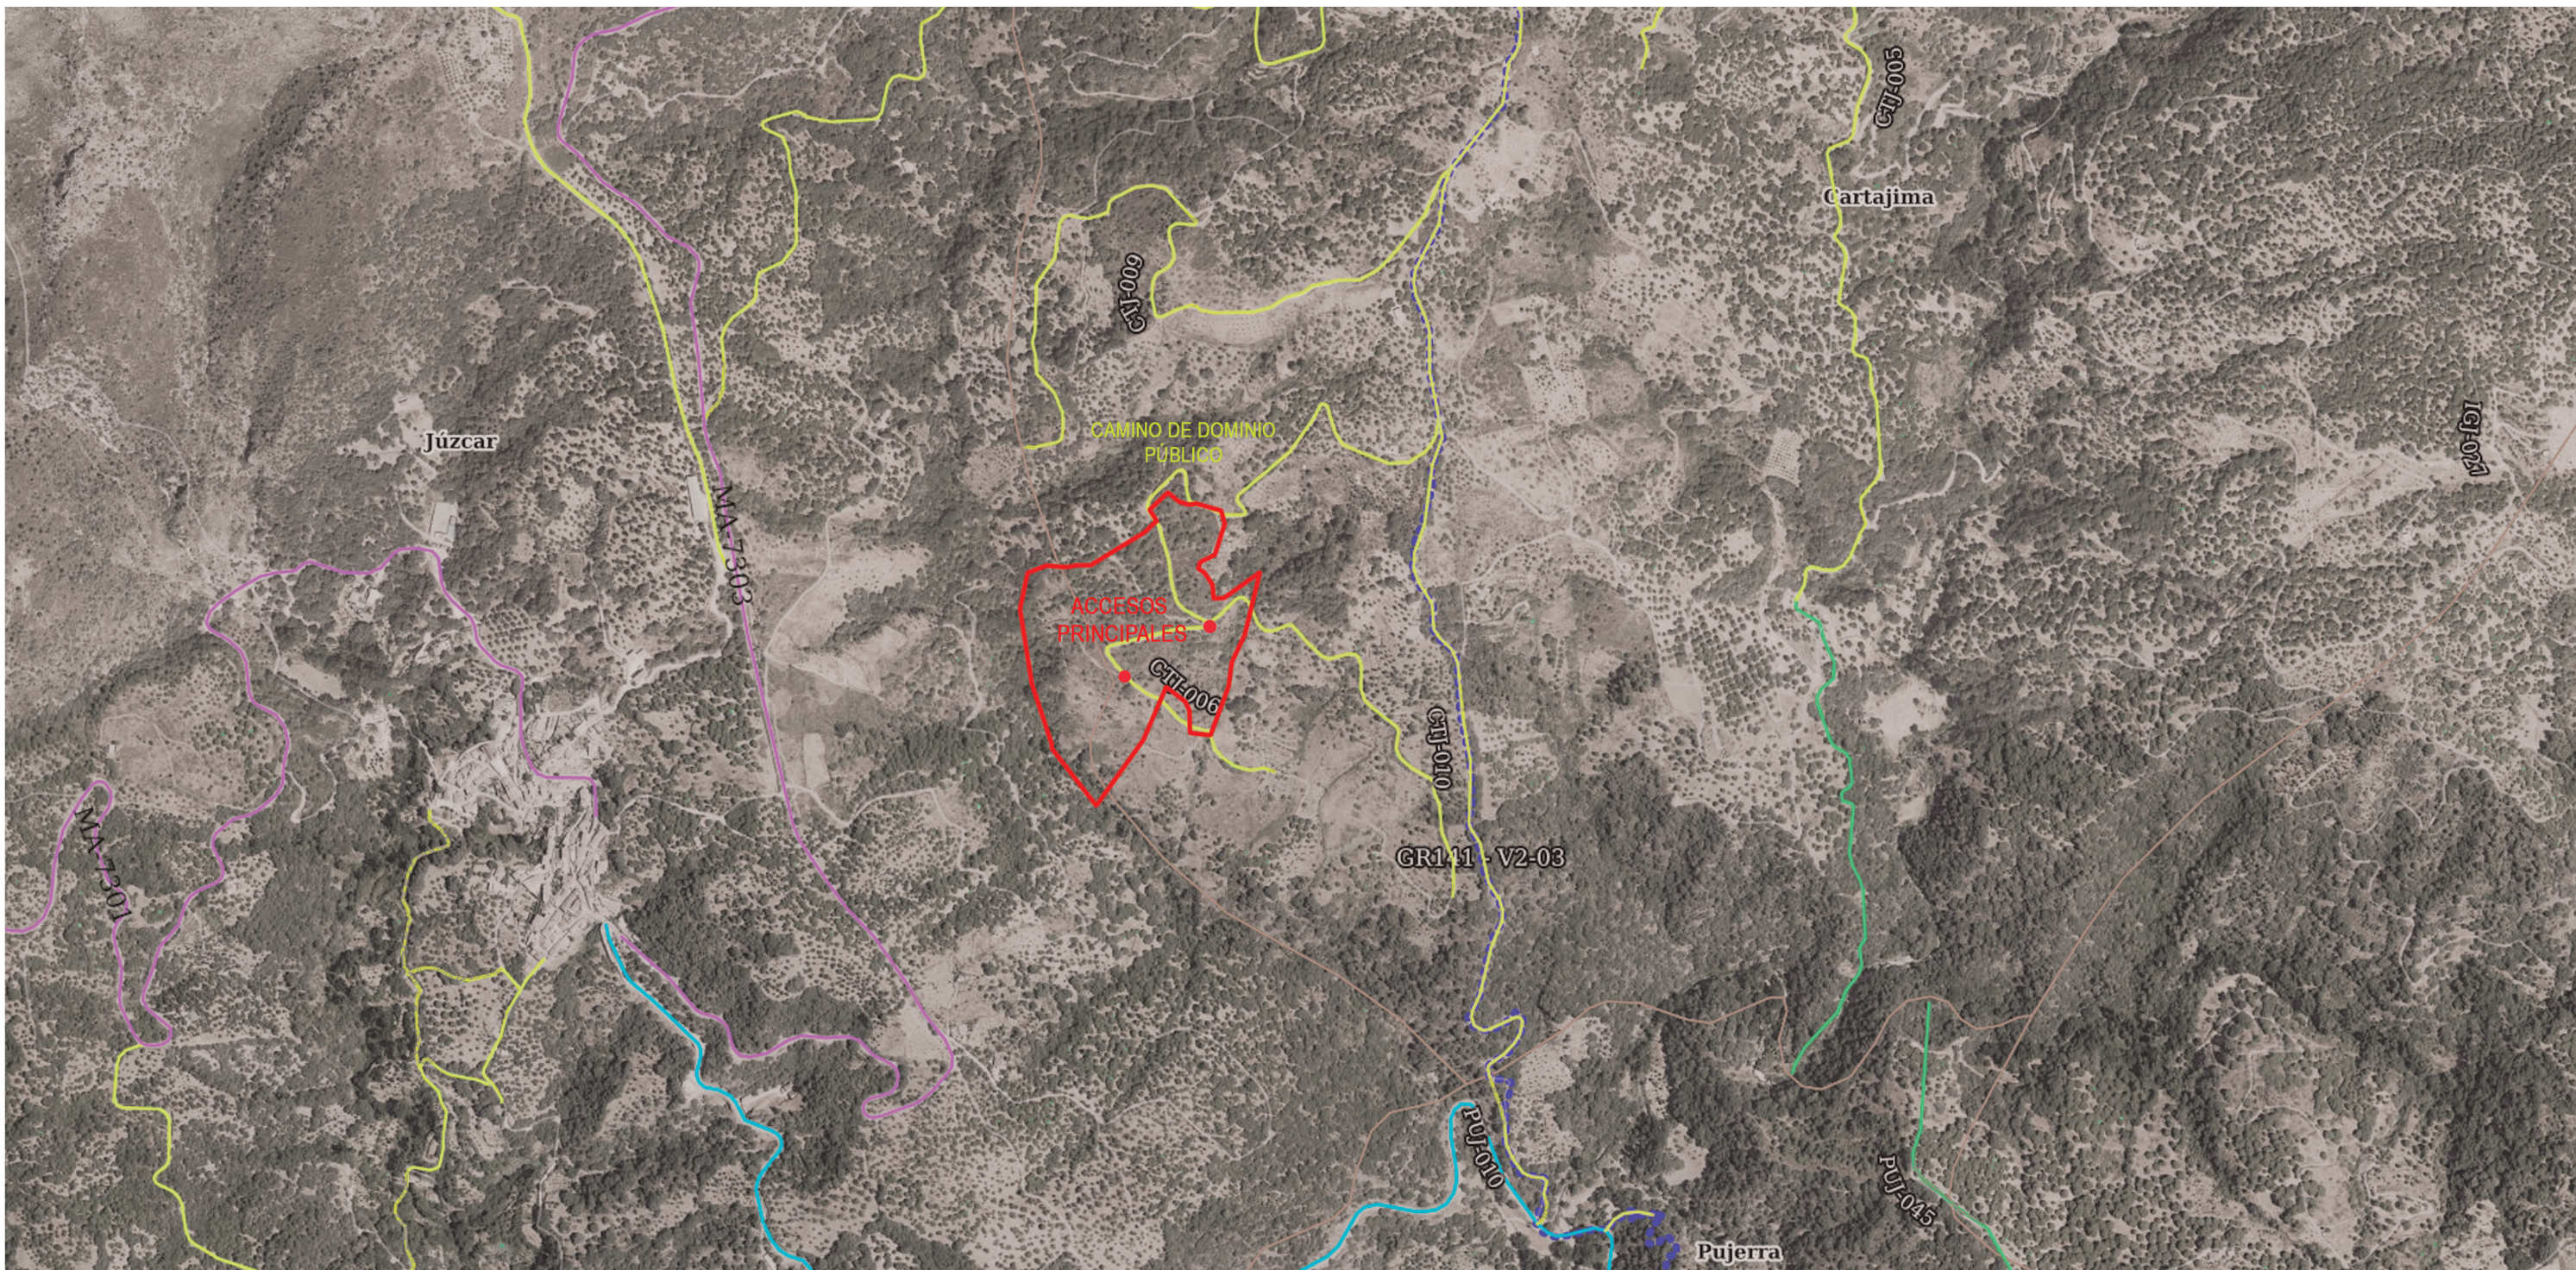



GEORREFERENCIACIÓN		
VIVIENDAS	COORDENADAS X	COORDENADAS Y
1	306740.5756	4055799.2924
2	306768.0434	4055766.5000
3	306802.4197	4055726.2040
4	306763.9811	4055716.5000
5	306797.0827	4055821.9461
6	306815.8738	4055763.0170
7	306687.1652	4055545.6045
8	306753.4668	4055548.0298
9	306778.3367	4055586.3048
10	306655.1918	4055770.3321
ÁREA ESPACIO COMÚN		
A	306730.4616	4055728.7911
B	306752.4272	4055747.7255
C	306728.2696	4055775.7506
D	306706.3039	4055756.8162
EDIFICACIÓN EXISTENTE		
E	306702.9296	4055705.3097
F	306706.0092	4055711.0229
G	306701.5314	4055713.4366
H	306698.4342	4055707.7329
POZO		
CENTRO CIRCUNFERENCIA	306684.1519	4055744.9828

LA GEO-REFERENCIACIÓN DE LAS ECO-VIVIENDAS MARCA EL PUNTO CENTRAL DEL ÁREA CIRCULAR DONDE SE UBICARÁ LA MISMA
SU DISPOSICIÓN EXACTA ESTARÁ EN FUNCIÓN DEL ESTUDIO DEL TERRENO

LOS ACCESOS A LAS ECO-VIVIENDAS SE REALIZARÁN MEDIANTE VEREDAS DE MÍNIMO IMPACTO DESDE LOS CAMINOS INTERIORES DE PARCELA Y LOS ACCESOS EXTERIORES DEL CAMINO DE DOMINIO PÚBLICO

1 KM DISTANCIA MUNICIPIO MÁS CERCANO (JÚZCAR)
2,2 KM DISTANCIA MUNICIPIO PERTENECIENTE (CARTAJIMA)

- POZO Y MANANTIAL
- ACOMETIDA ABASTECIMIENTO DE AGUA
- DA
- LÍNEA DE MEDÍA TENSIÓN
- SERVIDUMBRE LÍNEA DE MEDIA TENSIÓN
- TORRETA LÍNEA DE MEDIA TENSIÓN