

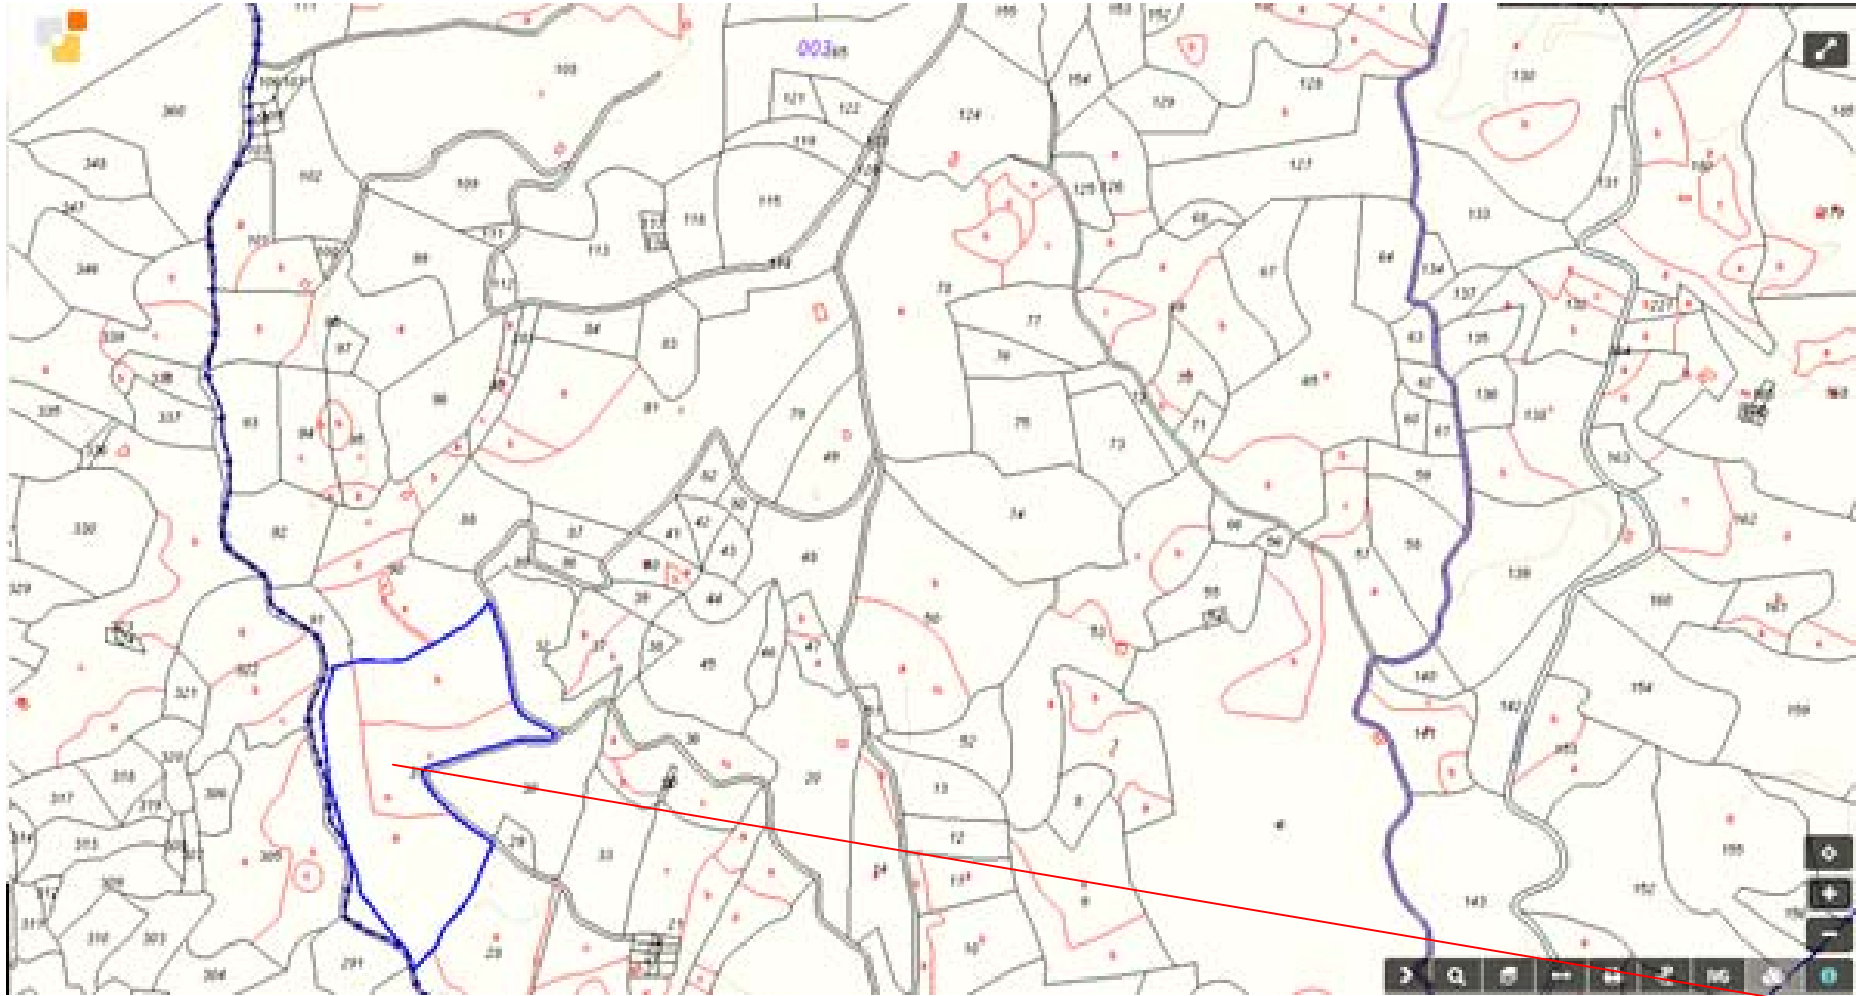


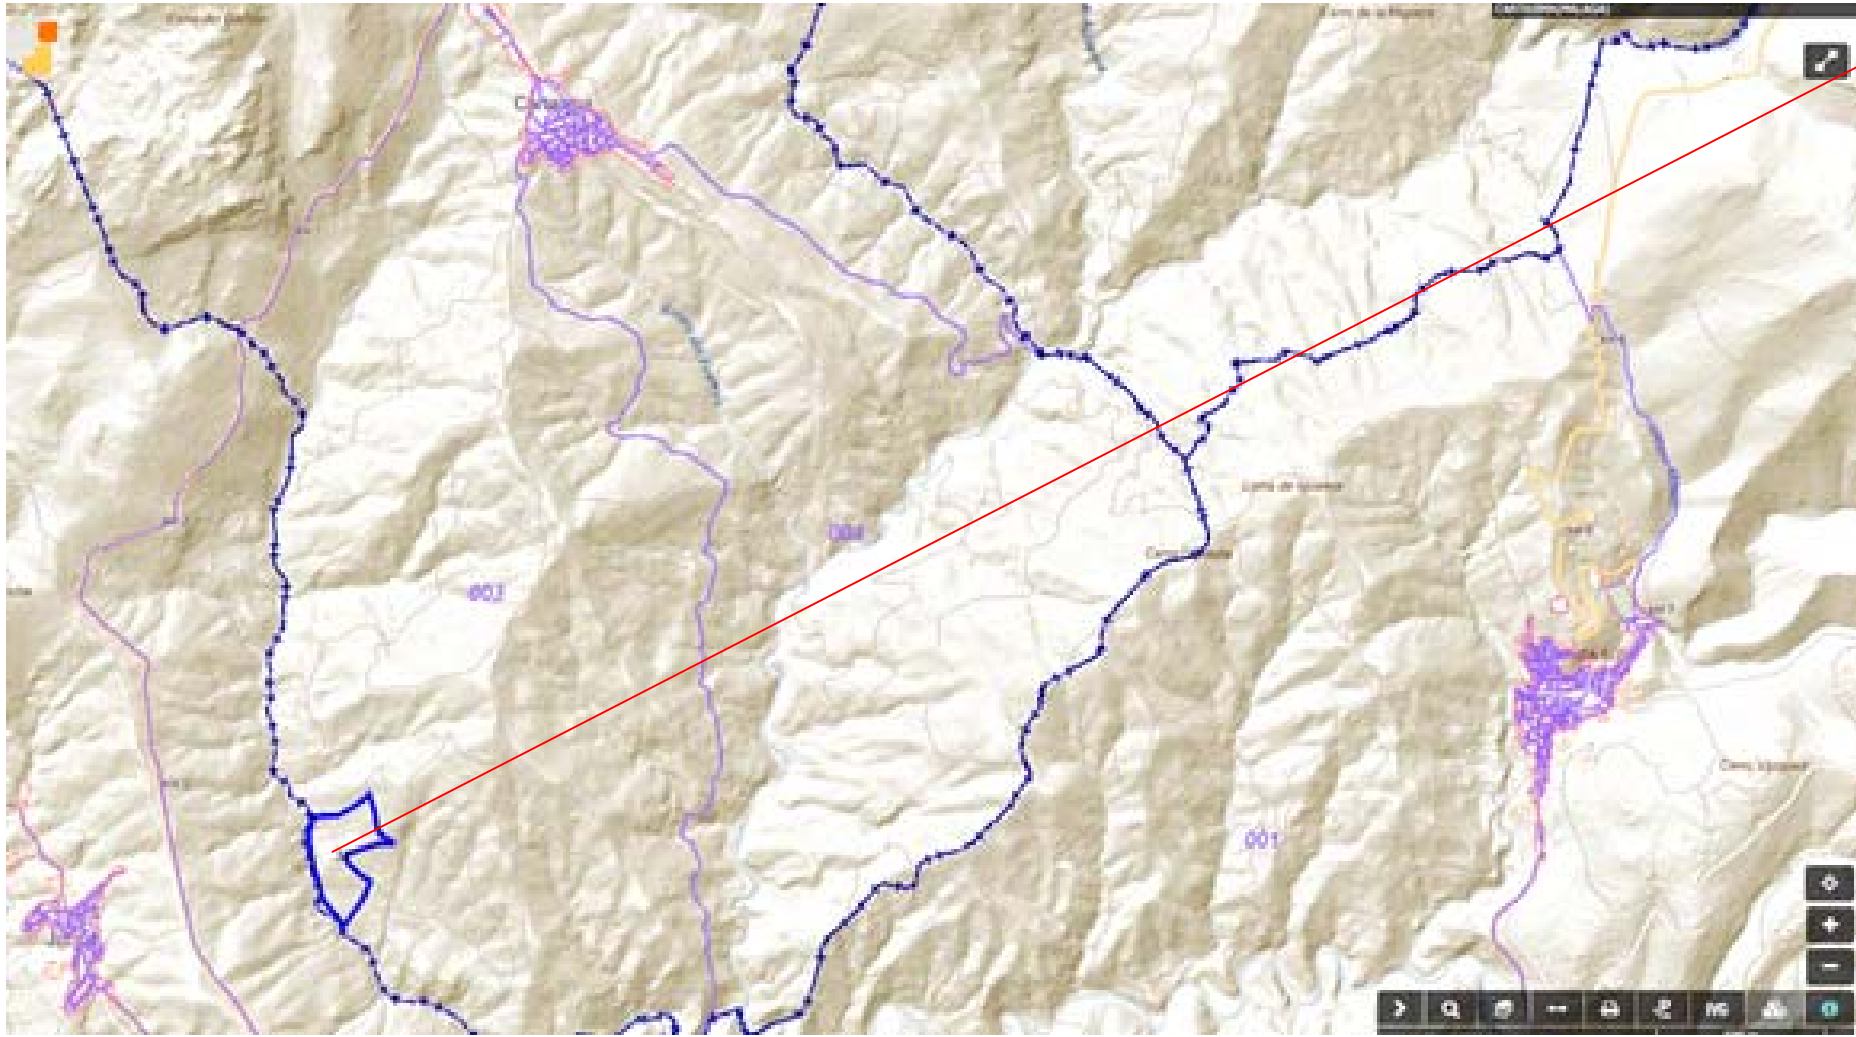

SITUACIÓN

PROYECTO TÉCNICO DE REFORMA DE EDIFICACIÓN
SITA EN POLÍGONO 3, PARCELA 31 DEL TÉRMINO
MUNICIPAL DE CARTAJIMA (MÁLAGA)

SITUACIÓN

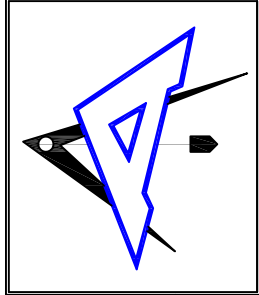


ESCALA: S/E

FECHA: NOVIEMBRE 2020


PROMOTOR: D. EDUARDO J. CORVACHO DE LA TORRE
DNA. ALMUDENA BERROCAL RAMOS

Arquitecto Técnico / Ingeniero de la Edificación.


Juan Manuel Morales Sánchez

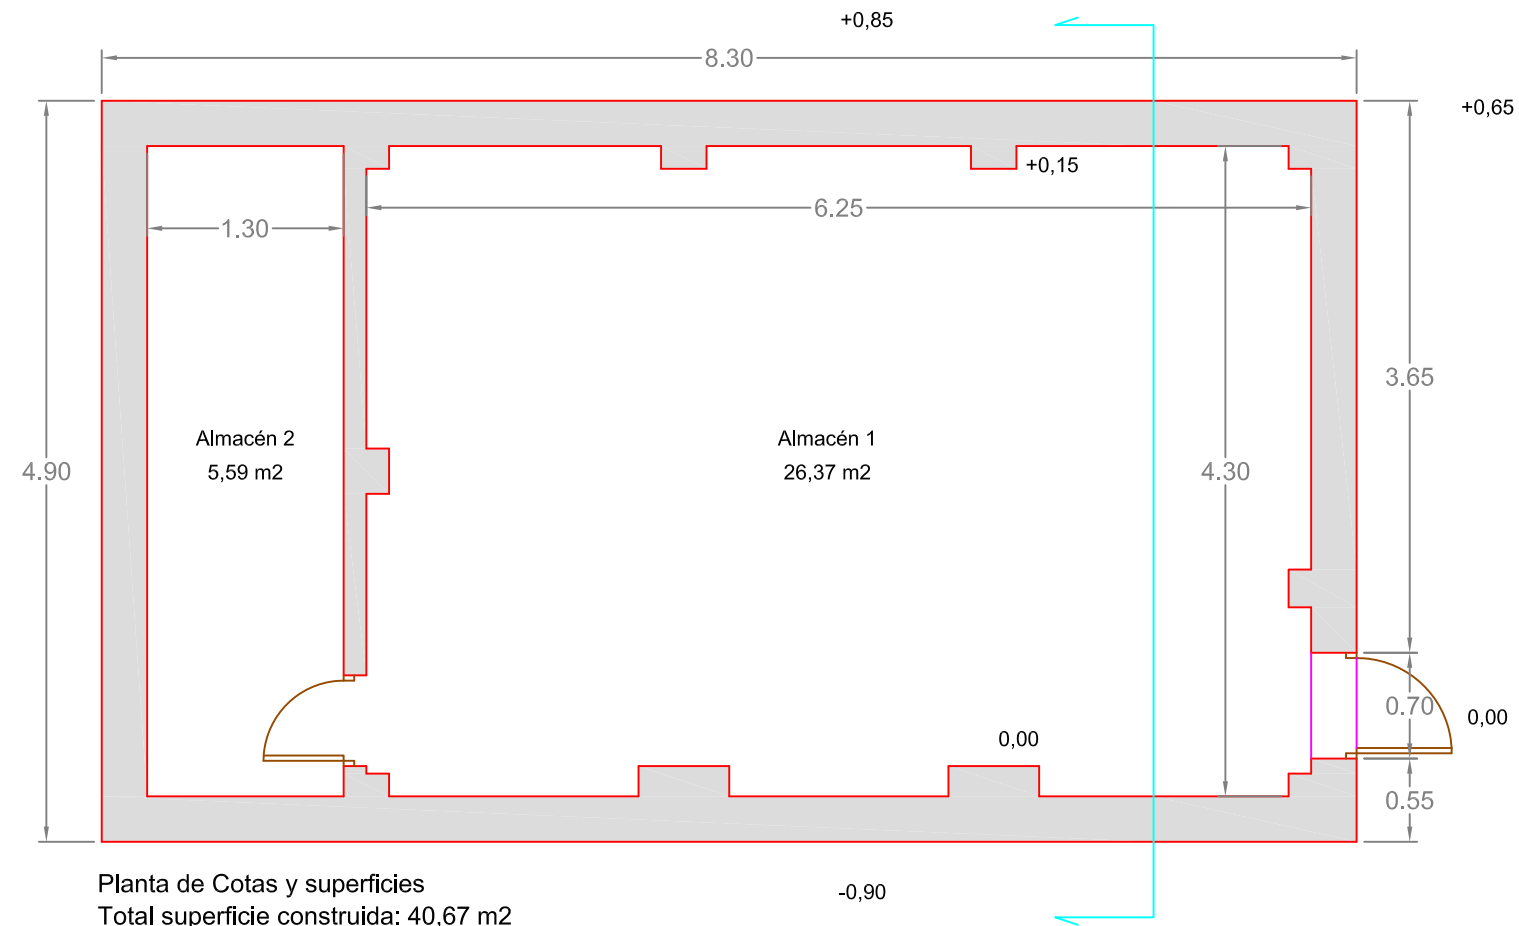


Planta de Cotas y superficies
Total superficie construida: 40,67 m2

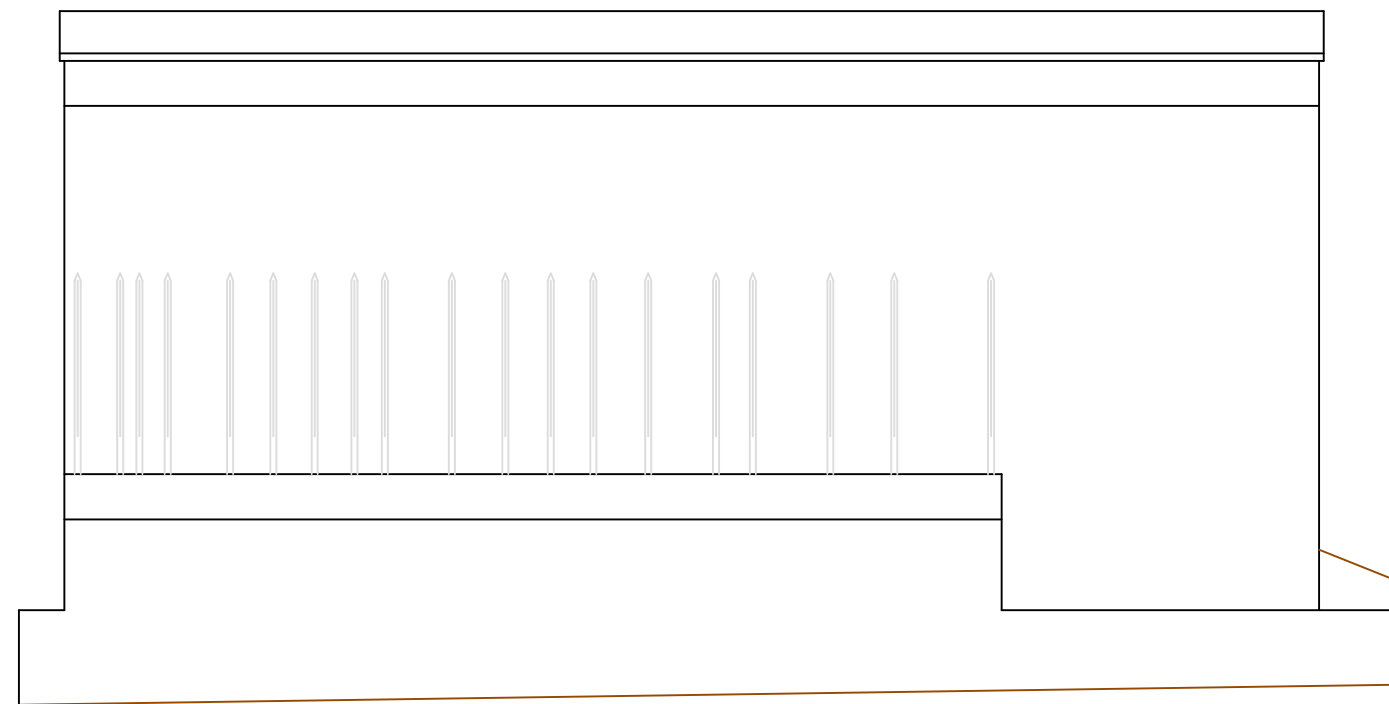

Alzado Lateral

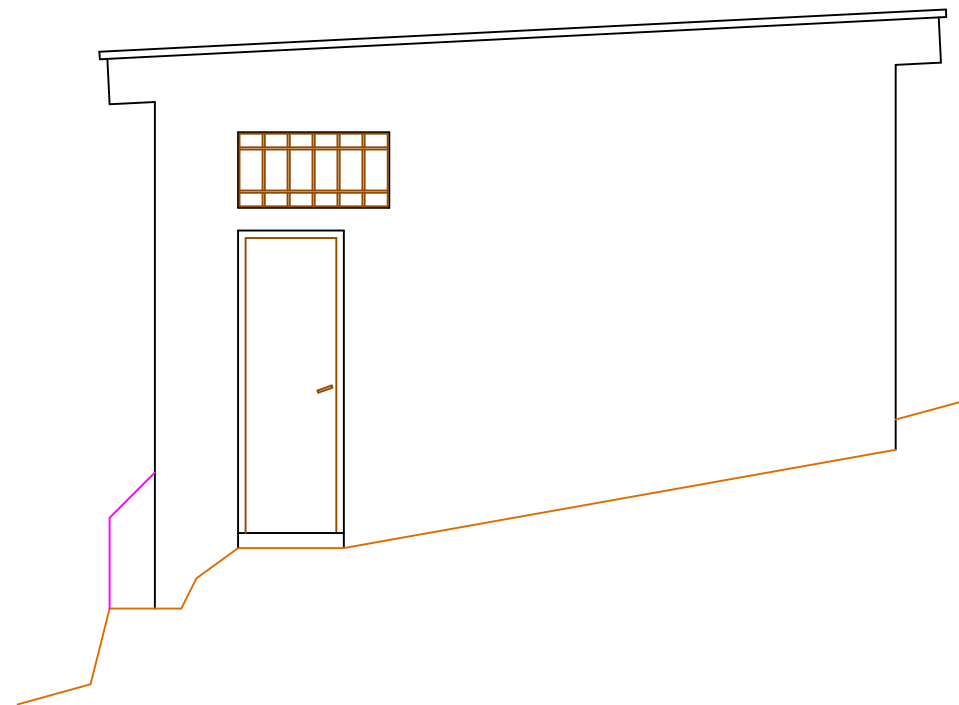


Alzado Principal

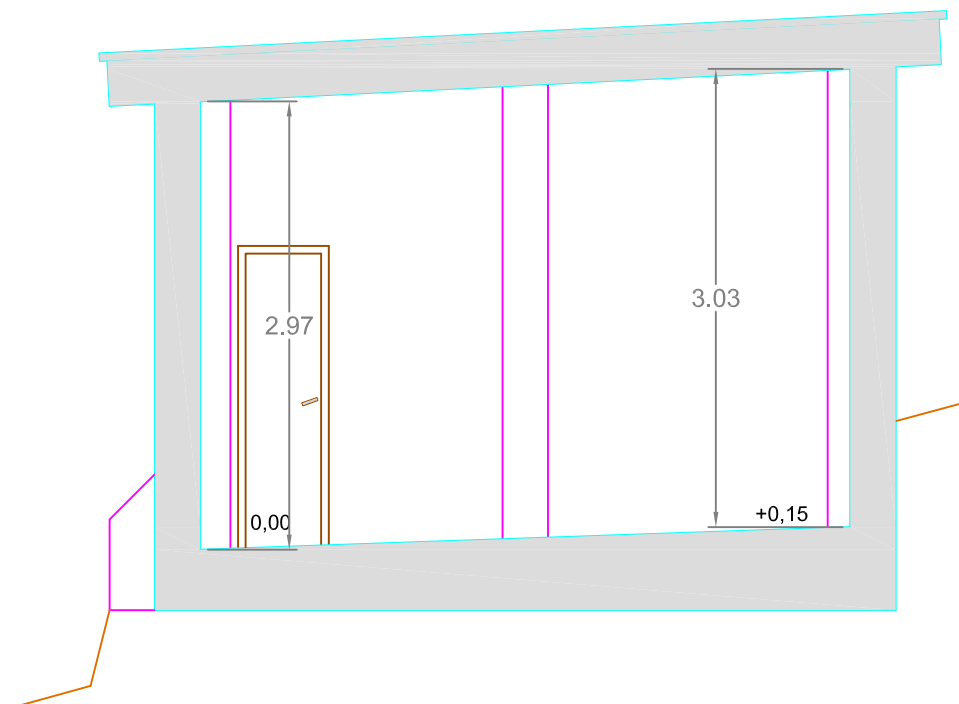


Sección

Arquitecto Técnico / Ingeniero de la Edificación.		Juan Manuel Morales Sánchez	
ESCALA: 1/50		FECHA: NOVIEMBRE 2020	
PROMOTOR: D. EDUARDO J. CORVACHO DE LA TORRE DÑA. ALMUDENA BERROCAL RAMOS		2	
PROYECTO TÉCNICO DE REFORMA DE EDIFICACIÓN SITA EN POLÍGONO 3, PARCELA 31 DEL TÉRMINO MUNICIPAL DE CARTAJIMA (MÁLAGA)			
ESTADO ACTUAL: PLANTA DE COTAS, ALZADOS Y SECCIÓN			


EL PRESENTE DOCUMENTO ES COPIA DE SU ORIGINAL DEL QUE ES AUTOR JUAN MANUEL MORALES SANCHEZ. SU UTILIZACIÓN TOTAL O PARCIAL, ASÍ COMO CUALQUIER REPRODUCCIÓN O CESIÓN A TERCEROS, REQUERIRÁ LA PRESENTACIÓN EXPRESA DE SU AUTOREDAD EN TODO CASO PROHIBIDA CUALQUIER MODIFICACIÓN MATERIAL DEL MISMO.

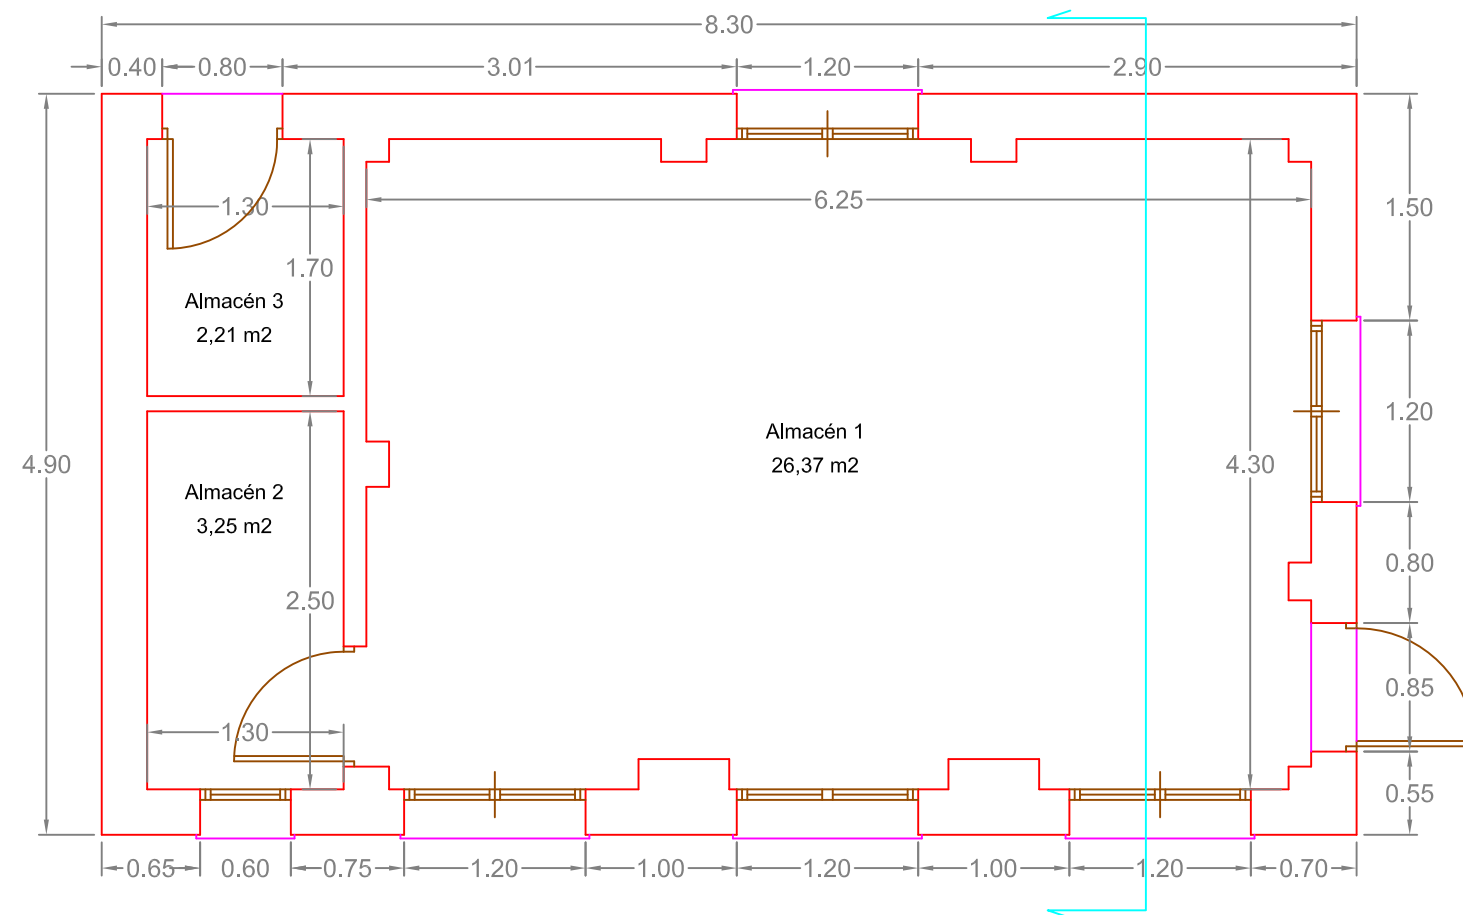


Planta de Cotas y superficies
Total superficie construida: 40,67 m2

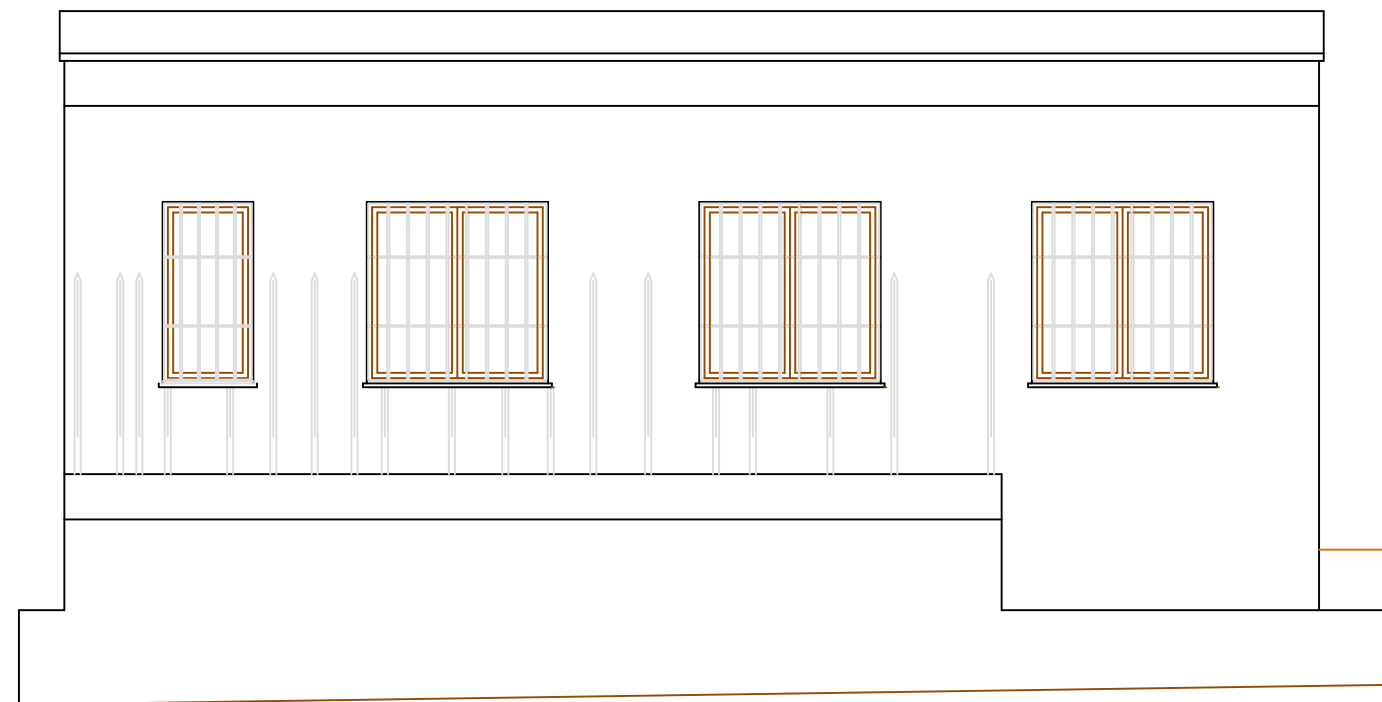

Alzado Lateral

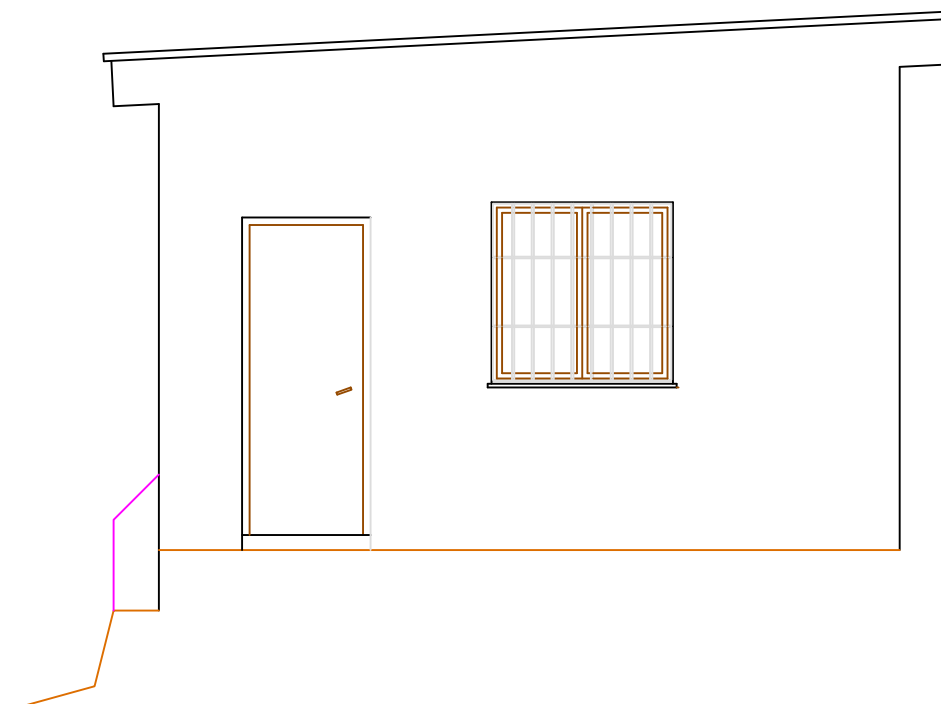


Alzado Principal

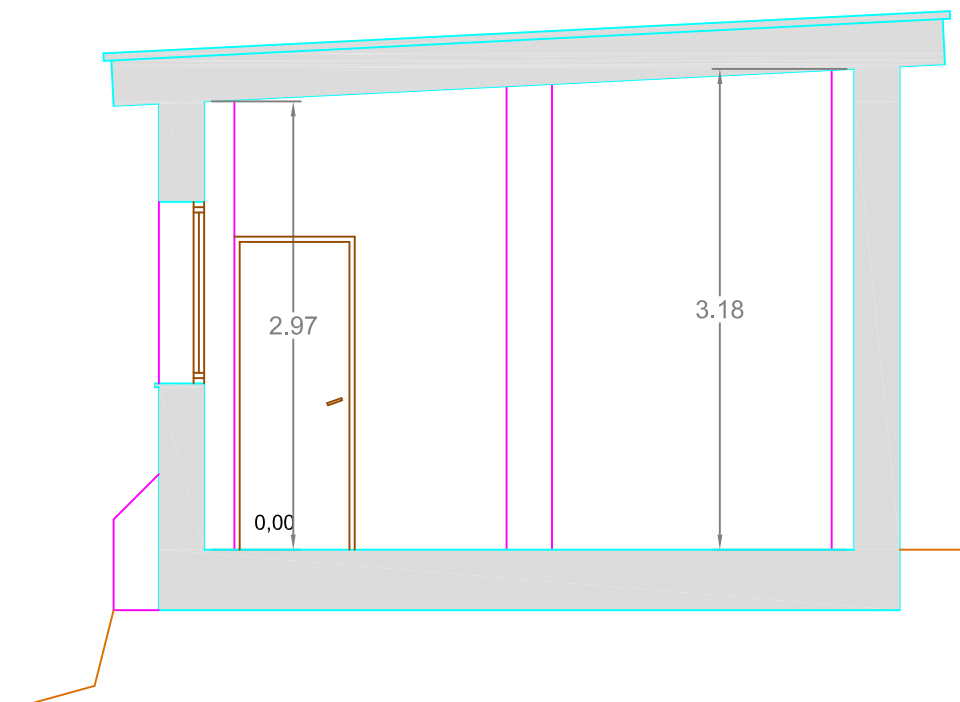

Sección

Arquitecto Técnico / Ingeniero de la Edificación. Juan Manuel Morales Sánchez	
ESCALA: 1/50	FECHA: NOVIEMBRE 2020
PROMOTOR: D. EDUARDO J. CORVACHO DE LA TORRE DÑA. ALMUDENA BERROCAL RAMOS	
3	
PROYECTO TÉCNICO DE REFORMA DE EDIFICACIÓN SITA EN POLÍGONO 3, PARCELA 31 DEL TÉRMINO MUNICIPAL DE CARTAJIMA (MÁLAGA)	
ESTADO REFORMADO: PLANTA DE COTAS, ALZADOS Y SECCIÓN	

EL PRESENTE DOCUMENTO ES COPIA DE SU ORIGINAL DEL QUE ES AUTÓR JUAN MANUEL MORALES SÁNCHEZ. SU UTILIZACIÓN TOTAL O PARCIAL, ASÍ COMO CUALQUIER REPRODUCCIÓN O DISEÑO A TERCEROS, REQUERIRÁ LA PRESENTACIÓN EXPRESA DE SU AUTOREDAD EN TODO CASO PROHIBIDA CUALQUIER MODIFICACIÓN MATERIAL DEL MISMO.

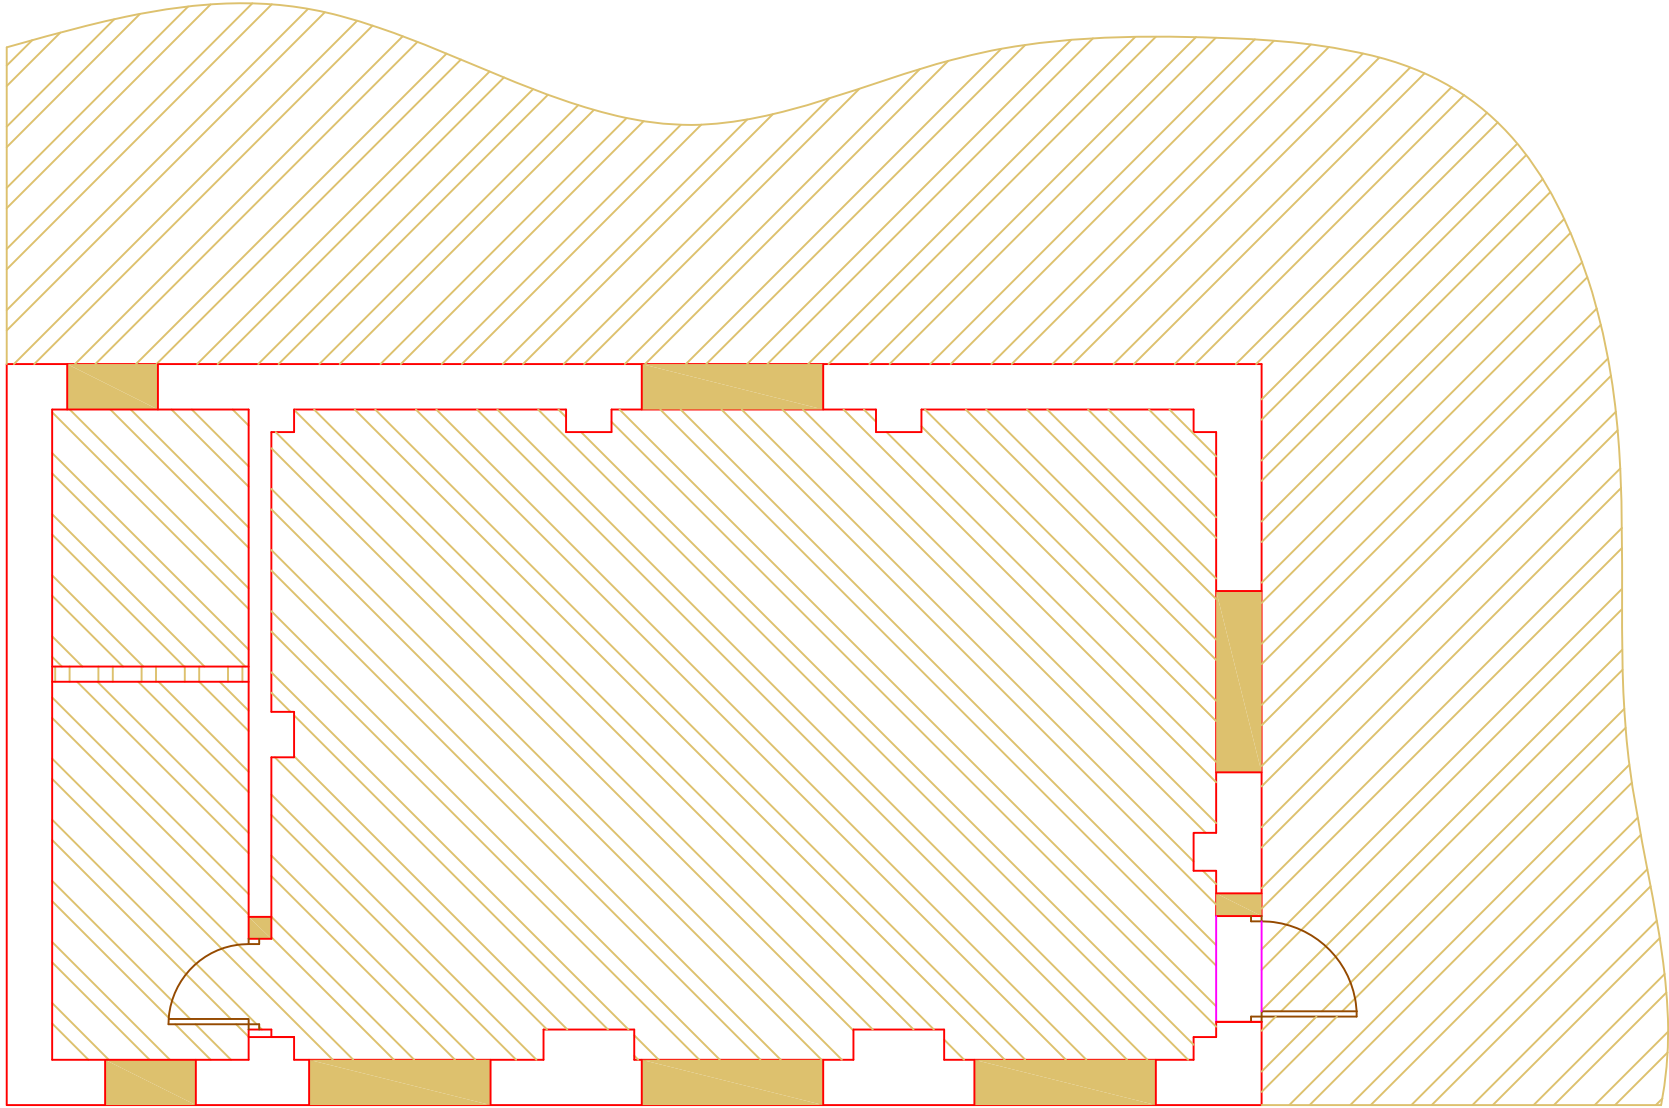


Planta de Actuaciones

-  Rebaje y nivelación de terreno
-  Demolición de fábrica para apertura de hueco
-  Demolición de fábrica para apertura de hueco
-  Nivelación solera de hormigón

PROYECTO TÉCNICO DE REFORMA DE EDIFICACIÓN
SITA EN POLÍGONO 3, PARCELA 31 DEL TÉRMINO
MUNICIPAL DE CARTAJIMA (MÁLAGA)

PLANTA DE ACTUACIONES

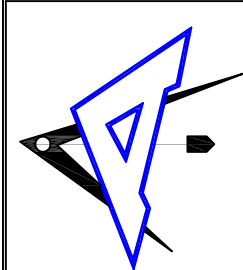


ESCALA: 1/50
FECHA: NOVIEMBRE 2020

4

PROMOTOR: D. EDUARDO J. CORVACHO DE LA TORRE
DÑA. ALMUDENA BERROCAL RAMOS

Arquitecto Técnico / Ingeniero de la Edificación.

Juan Manuel Morales Sánchez

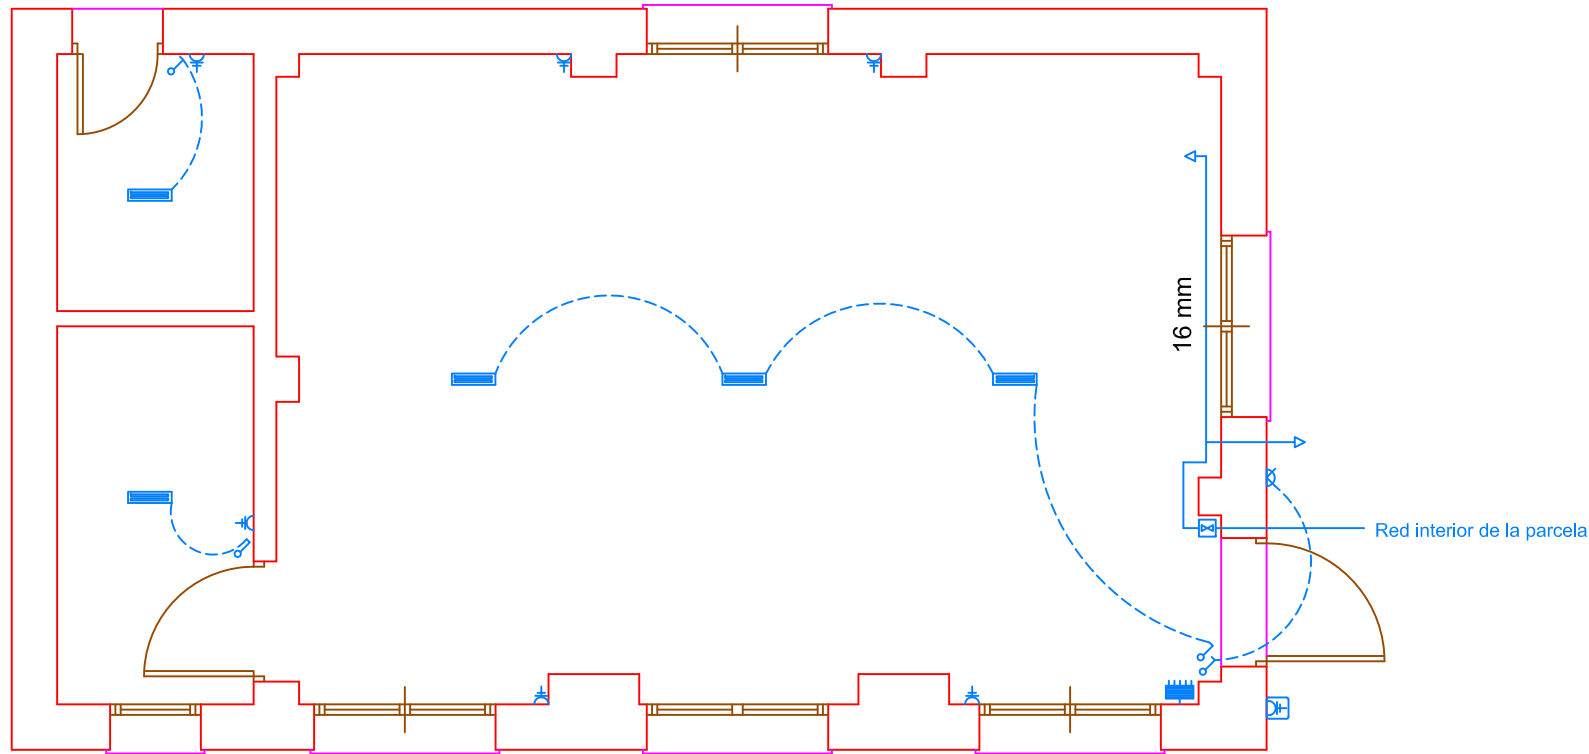

Planta de Instalaciones


LEYENDA DE FONTANERÍA

- LLAVE DE PASO GENERAL
- DISPOSITIVO ANTIARIEETE
- DISPOSITIVO ACUMULADOR
- GRUPO MOTOBOMBA
- CALENTADOR INSTANTÁNEO
- CONTADOR GENERAL
- DEPÓSITO - CALDERÍN
- LLAVE DE PASO
- TOMA O PUNTO DE AGUA
- A.F.S.
- A.C.S.
- VÁLVULA REDUCTORA AUT.
- DEPÓSITO PARTIDOR ANTICAL
- FLUXOR
- VÁLVULA ANTIRRETORNO
- TERMO ACUMULADOR
- CALENTADOR ACUMULADOR CENTRALIZADO
- MONTANTES

LEYENDA DE ELECTRICIDAD

- CAJA GENERAL DE PROTECCIÓN
- CUADRO GENERAL MANDO Y PROTECCIÓN
- VIDEO PORTERO
- INTERRUPTOR SIMPLE
- INTERRUPTOR CONMUTADO
- INTERRUPTOR DE CRUCE
- TOMA DE CORRIENTE DE 10 A.
- TOMA DE CORRIENTE DE 16/20 A.
- TOMA DE CORRIENTE DE 25 A.
- TOMA DE CORRIENTE ESTANCA
- PUNTO DE LUZ EN TECHO. 60 w
- FLUORESCENTE. 2x18 w
- TIMBRE
- PULSADOR
- RED DATOS
- TOMA DE TELÉFONO
- TOMA DE TELEVISIÓN
- EXTRACTOR
- DOWNLIGHT SUSPENDIDOS
- DOWNLIGHT ORIENTABLES
- PUNTO DE LUZ EN PARED. 40 w

TODOS LOS ENCHUFES HAN DE TENER TOMA A TIERRA

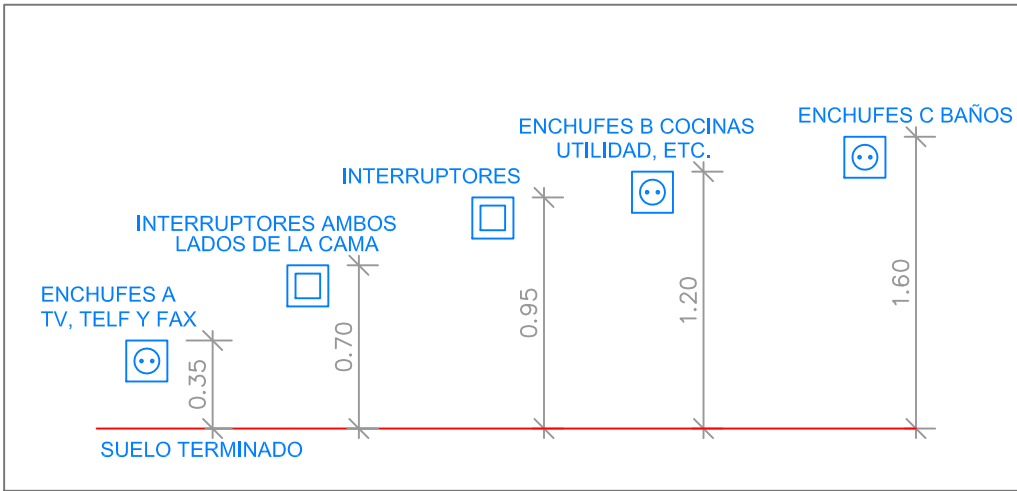

Arquitecto Técnico / Ingeniero de la Edificación.


Juan Manuel Morales Sánchez

5

ESCALA: 1/50


FECHA: NOVIEMBRE 2020

PROMOTOR: D. EDUARDO J. CORVACHO DE LA TORRE
DÑA. ALMUDENA BERROCAL RAMOS

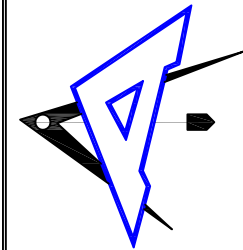


PROYECTO TÉCNICO DE REFORMA DE EDIFICACIÓN
SITA EN POLÍGONO 3, PARCELA 31 DEL TÉRMINO
MUNICIPAL DE CARTAJIMA (MÁLAGA)

PLANTA DE INSTALACIONES

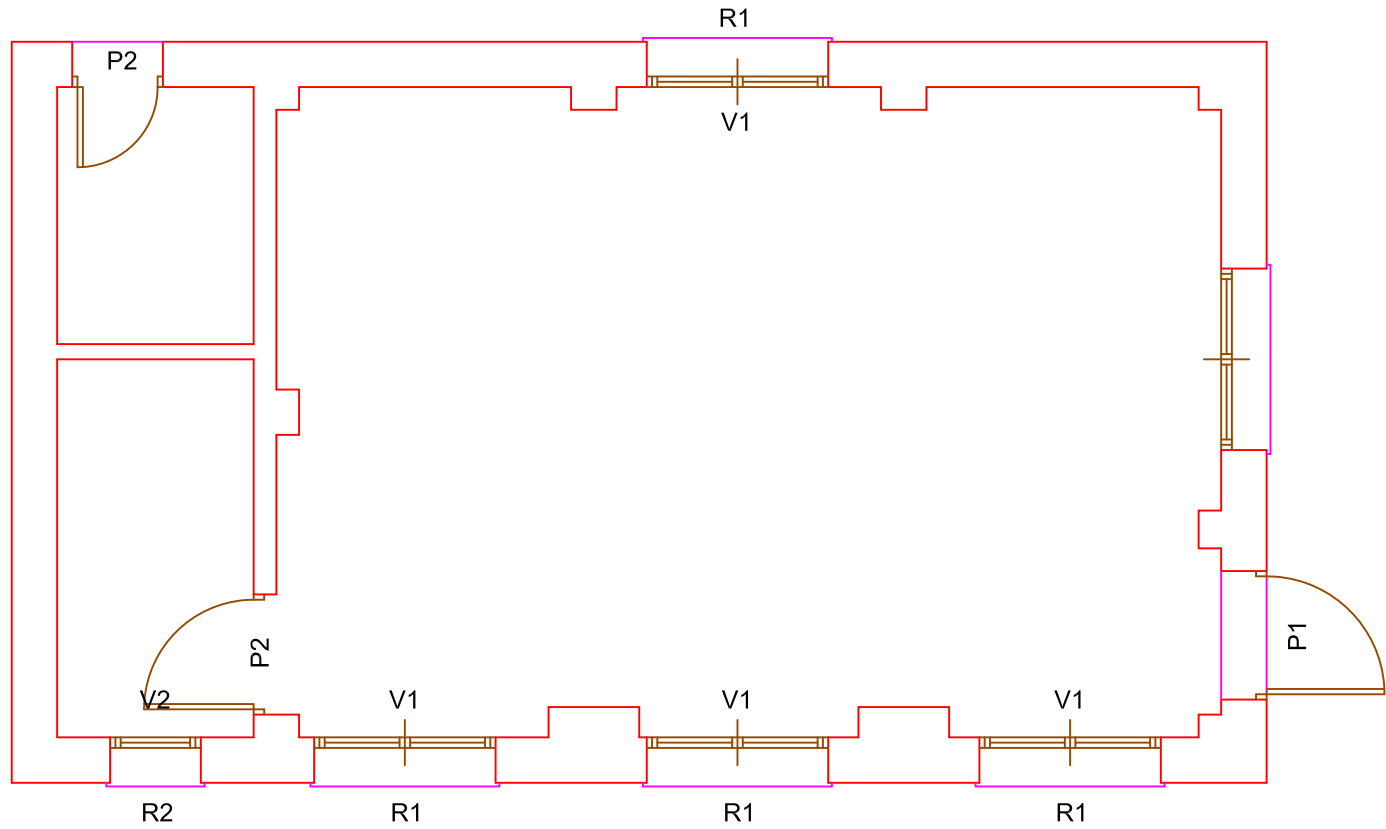

Planta de Instalaciones

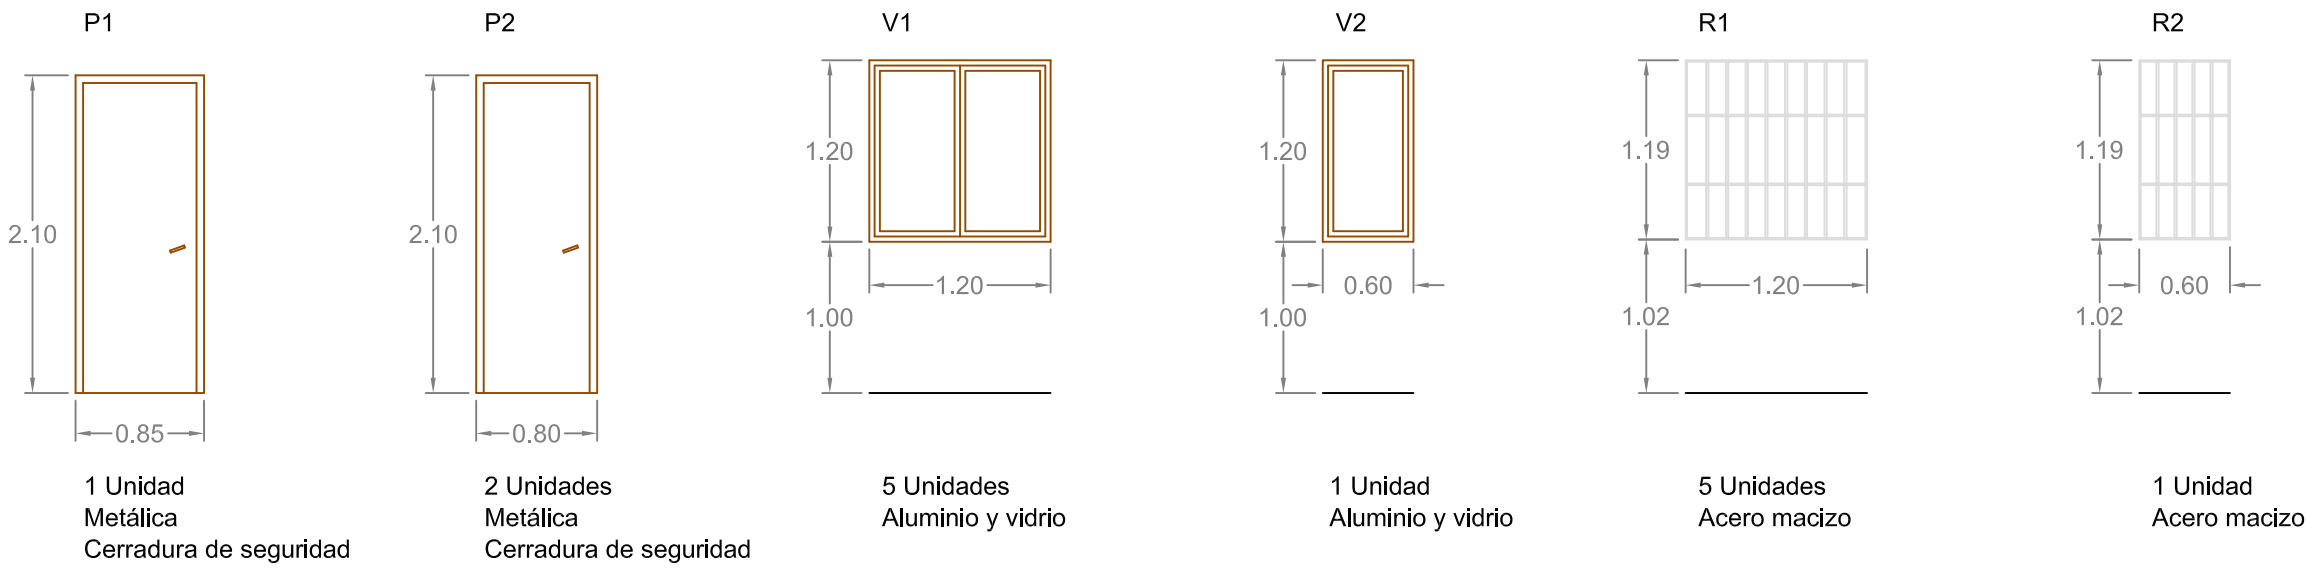

Arquitecto Técnico / Ingeniero de la Edificación. Juan Manuel Morales Sánchez	
6	
ESCALA: 1/50	FECHA: NOVIEMBRE 2020
PROMOTOR: D. EDUARDO J. CORVACHO DE LA TORRE DÑA. ALMUDENA BERROCAL RAMOS	
PROYECTO TÉCNICO DE REFORMA DE EDIFICACIÓN SITA EN POLÍGONO 3, PARCELA 31 DEL TÉRMINO MUNICIPAL DE CARTAJIMA (MÁLAGA)	
CARPINTERÍA	

EL PRESENTE DOCUMENTO ES COPIA DE SU ORIGINAL DEL QUE ES AUTOR JUAN MANUEL MORALES SANCHEZ, SU UTILIZACION TOTAL O PARCIAL, ASI COMO CUALQUIER REPRODUCCION O DESIN A TERCEROS, REQUERIRA LA PRETA AUTORIZACION EXPRESA DE SU AUTOREDANDO EN TODO CASO PROHIBIDA CUALQUIER MODIFICACION MATERIAL DEL MISMO