



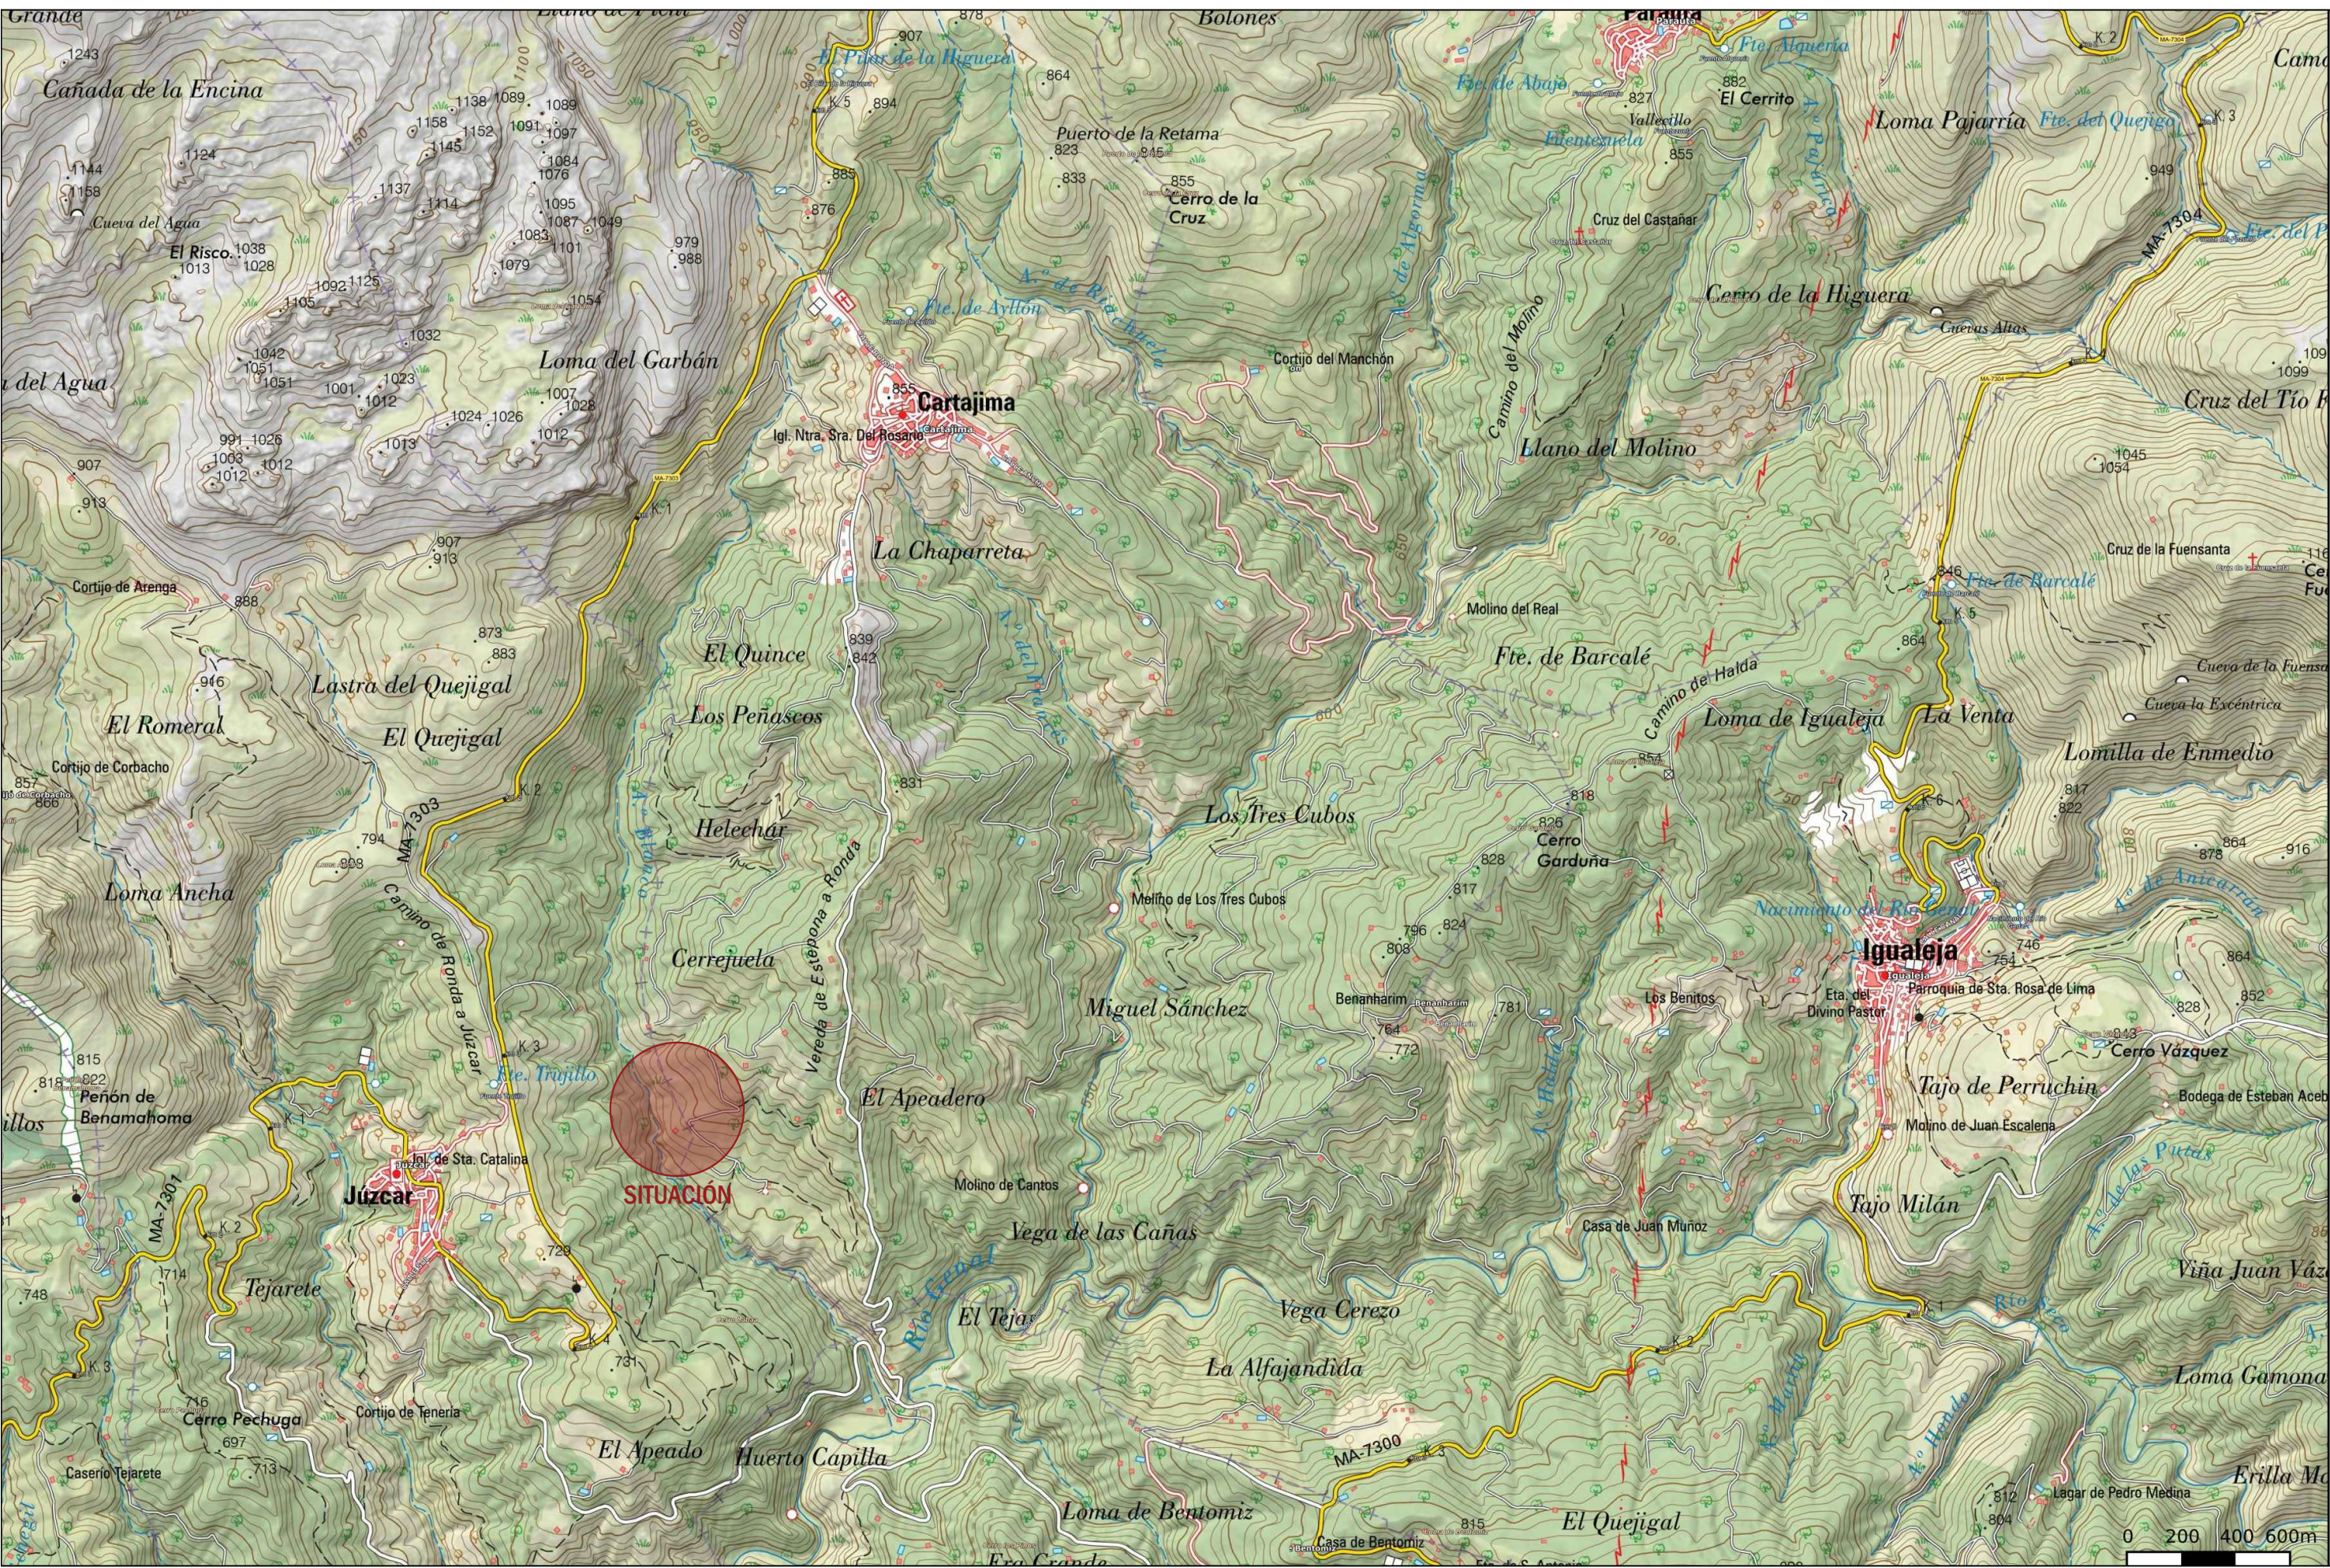

PLANO: SITUACIÓN EN EL TERRITORIO	
PROYECTO DE ACTUACIÓN CENTRO ECO-TURISMO EN VIÑA DE JUANES, TÉRMINO MUNICIPAL DE CARTAJIMA -MÁLAGA	
arquitecto: Rafael Segundo Navarro_colaborador: Miguel Orozco Martín	fecha: 12 de Septiembre de 2025

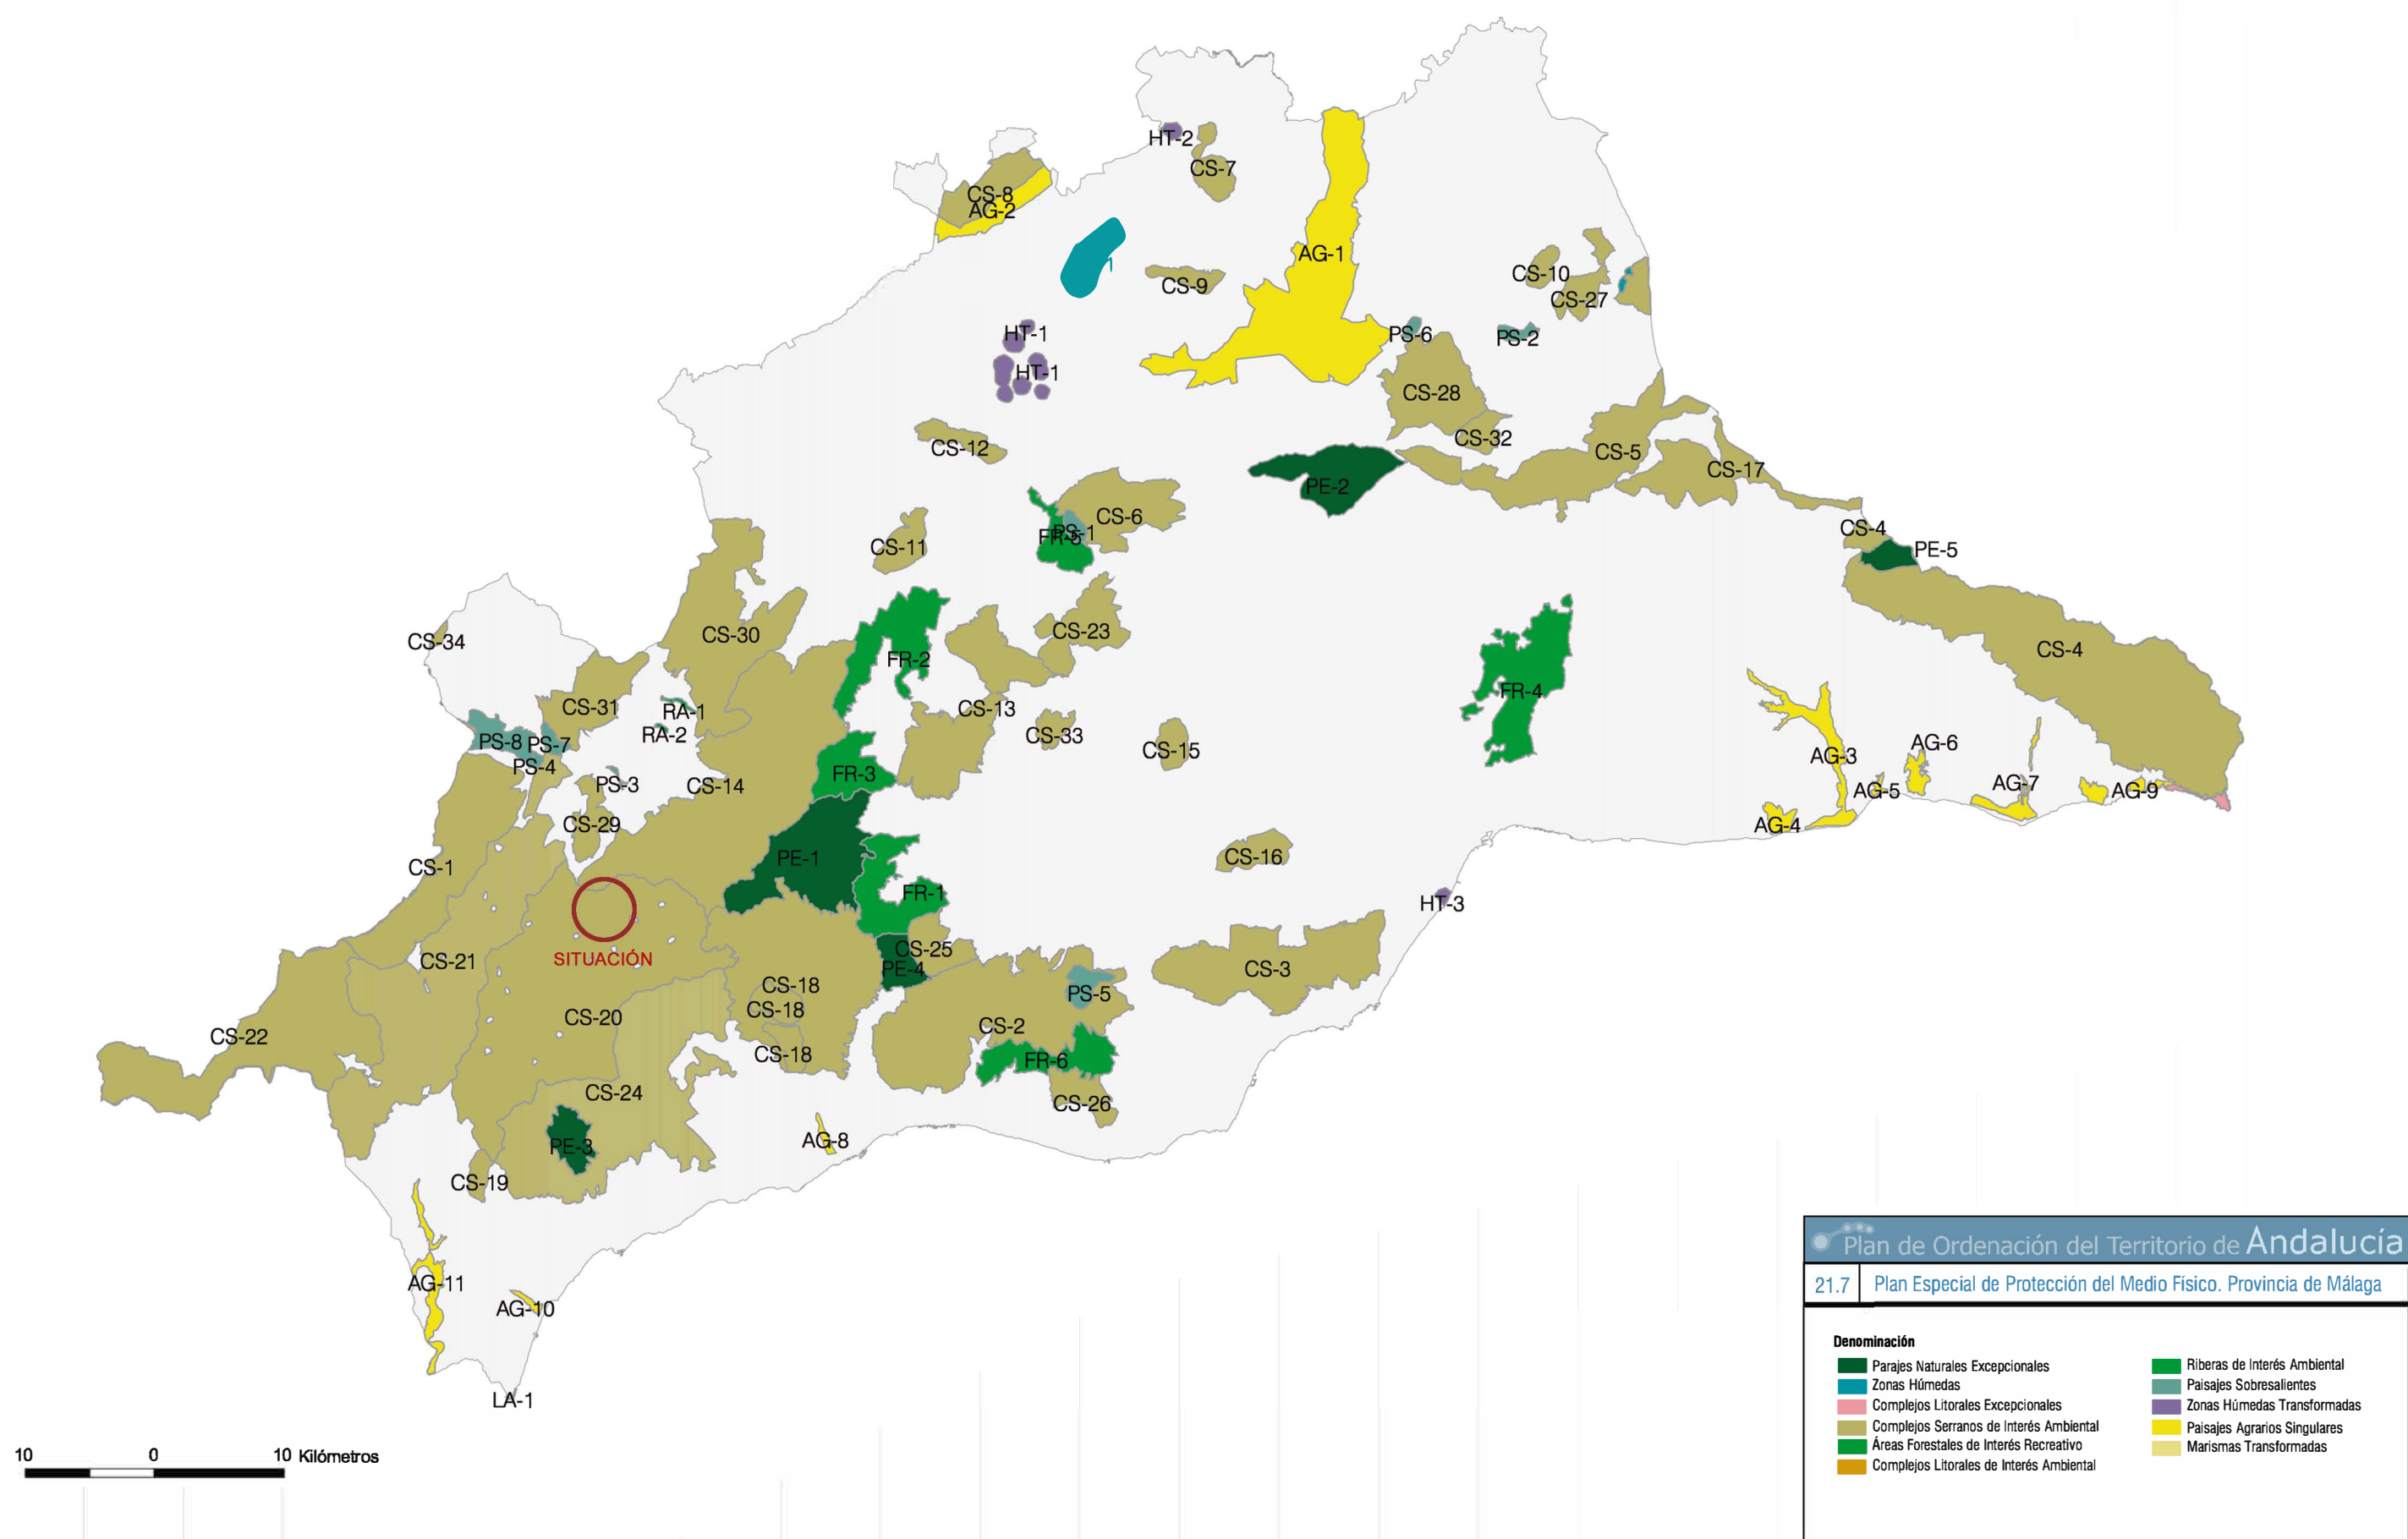


PLANO: SITUACIÓN EN EL PEPMF (PLAN ESPECIAL DE PROTECCIÓN DEL MEDIO FÍSICO)

PROYECTO DE ACTUACIÓN CENTRO ECO-TURISMO EN VIÑA DE JUANES, TÉRMINO MUNICIPAL DE CARTAJIMA -MÁLAGA

arquitecto: Rafael Segundo Navarro_colaborador: Miguel Orozco Martín

fecha: 12 de Septiembre de 2025

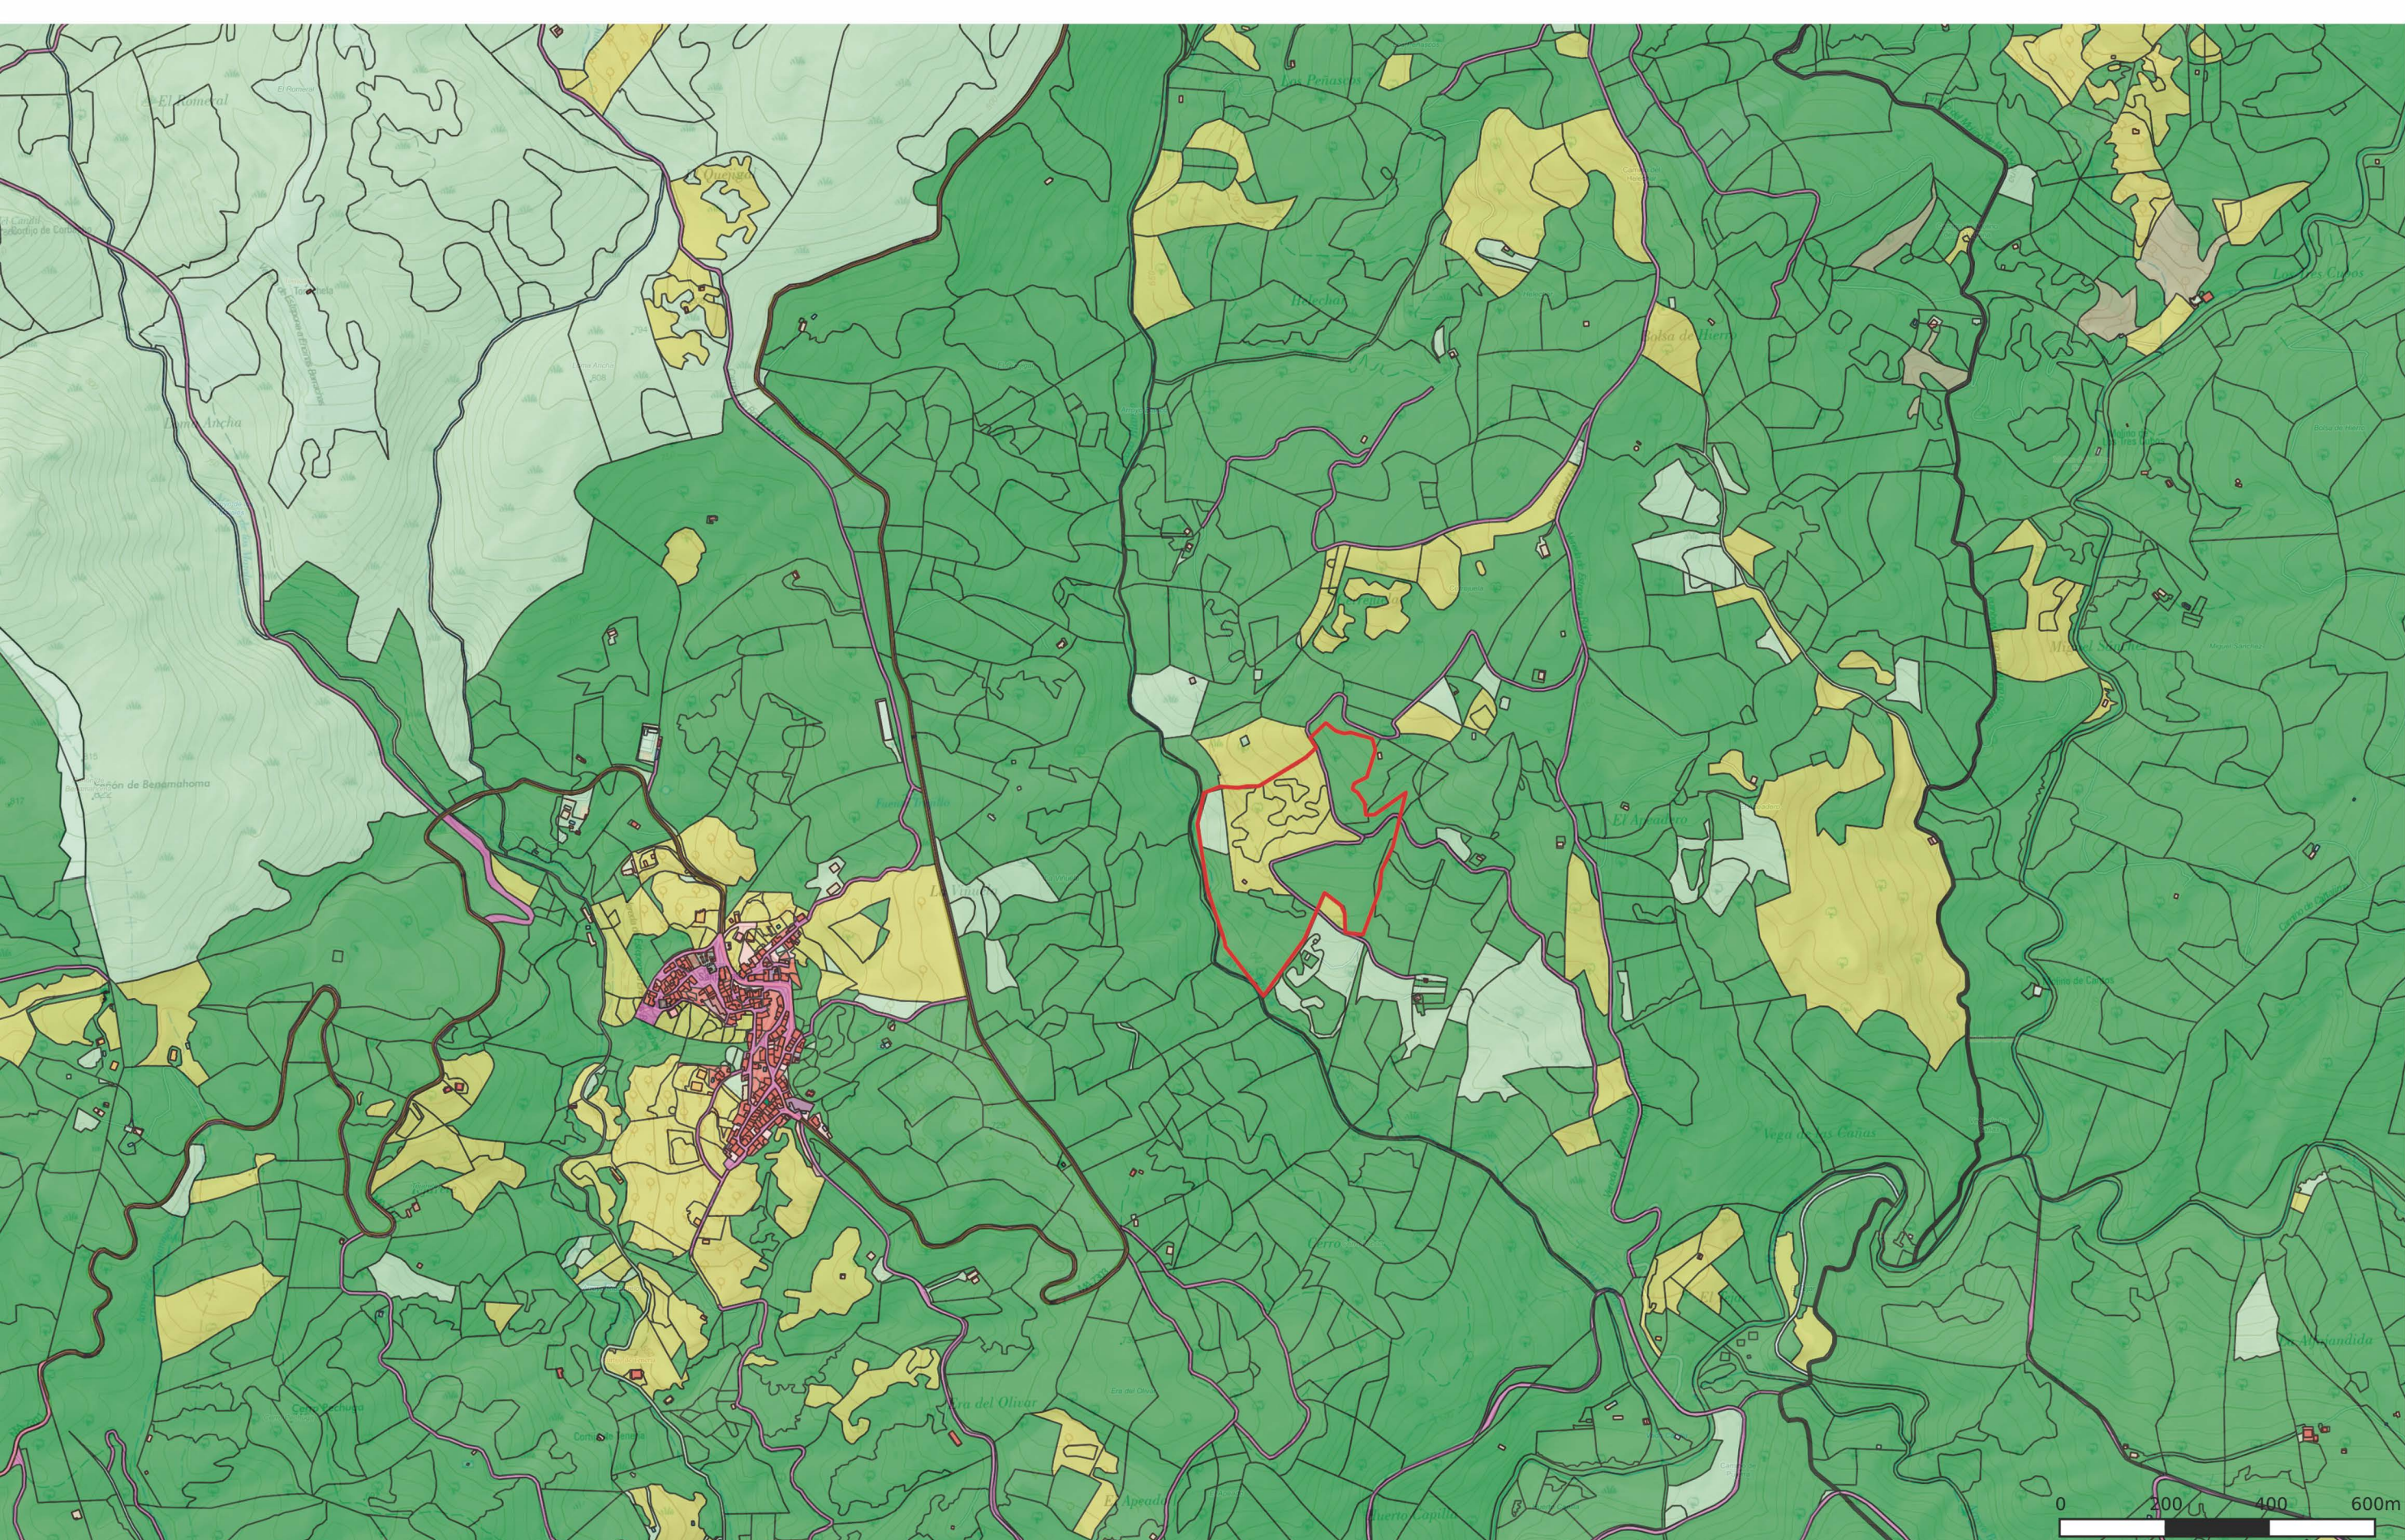

● USO AGRÍCOLA ● USO FORESTAL ● USO FORESTAL + OTRA ACTIVIDAD ECONÓMICA

PLANO: USOS DEL SUELO

PROYECTO DE ACTUACIÓN CENTRO ECO-TURISMO EN VIÑA DE JUANES, TÉRMINO MUNICIPAL DE CARTAJIMA - MÁLAGA

arquitecto: Rafael Segundo Navarro_colaborador: Miguel Orozco Martín

fecha: 12 de Septiembre de 2025




● OLIVAR ● FRUTALES NO CÍTRICOS ● CUBIERTA FORESTAL

PLANO: CUBIERTA VEGETAL


PROYECTO DE ACTUACIÓN CENTRO ECO-TURISMO EN VIÑA DE JUANES, TÉRMINO MUNICIPAL DE CARTAJIMA -MÁLAGA

arquitecto: Rafael Segundo Navarro_colaborador: Miguel Orozco Martín

fecha: 12 de Septiembre de 2025

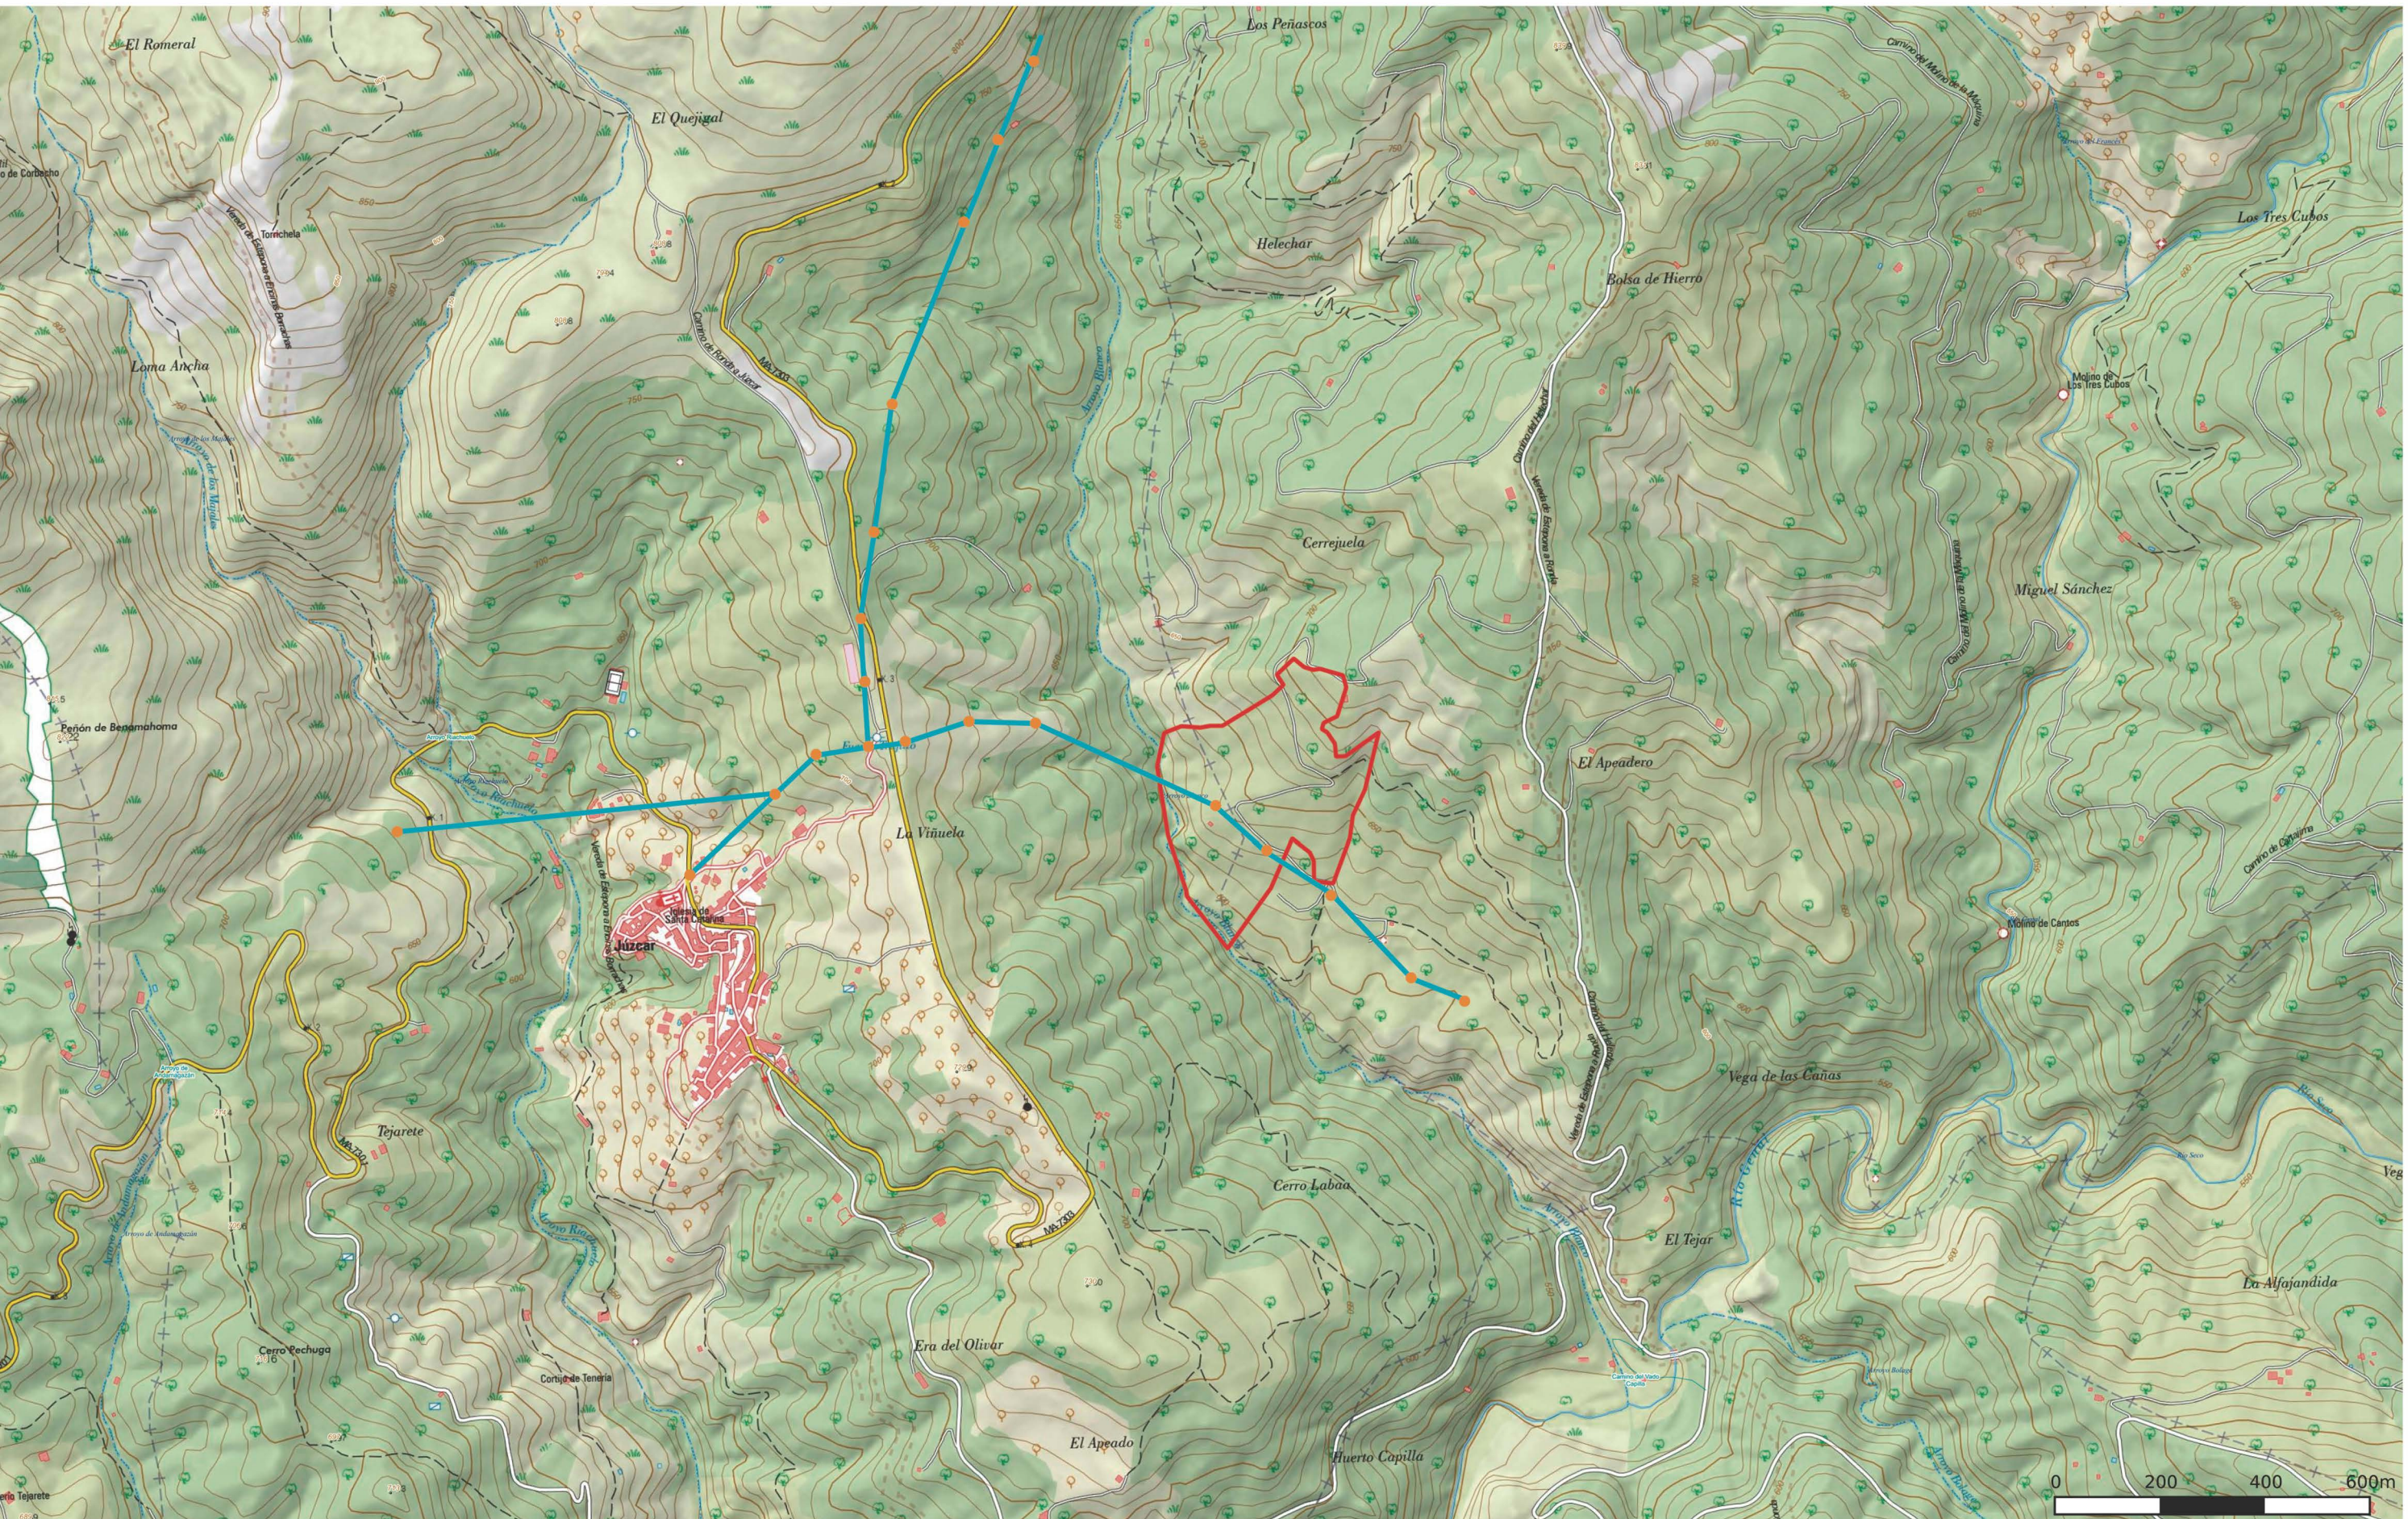

— LÍNEA DE MEDIA TENSIÓN (ÚNICA INFRAESTRUCTURA RELEVANTE EN LA PARCELA)

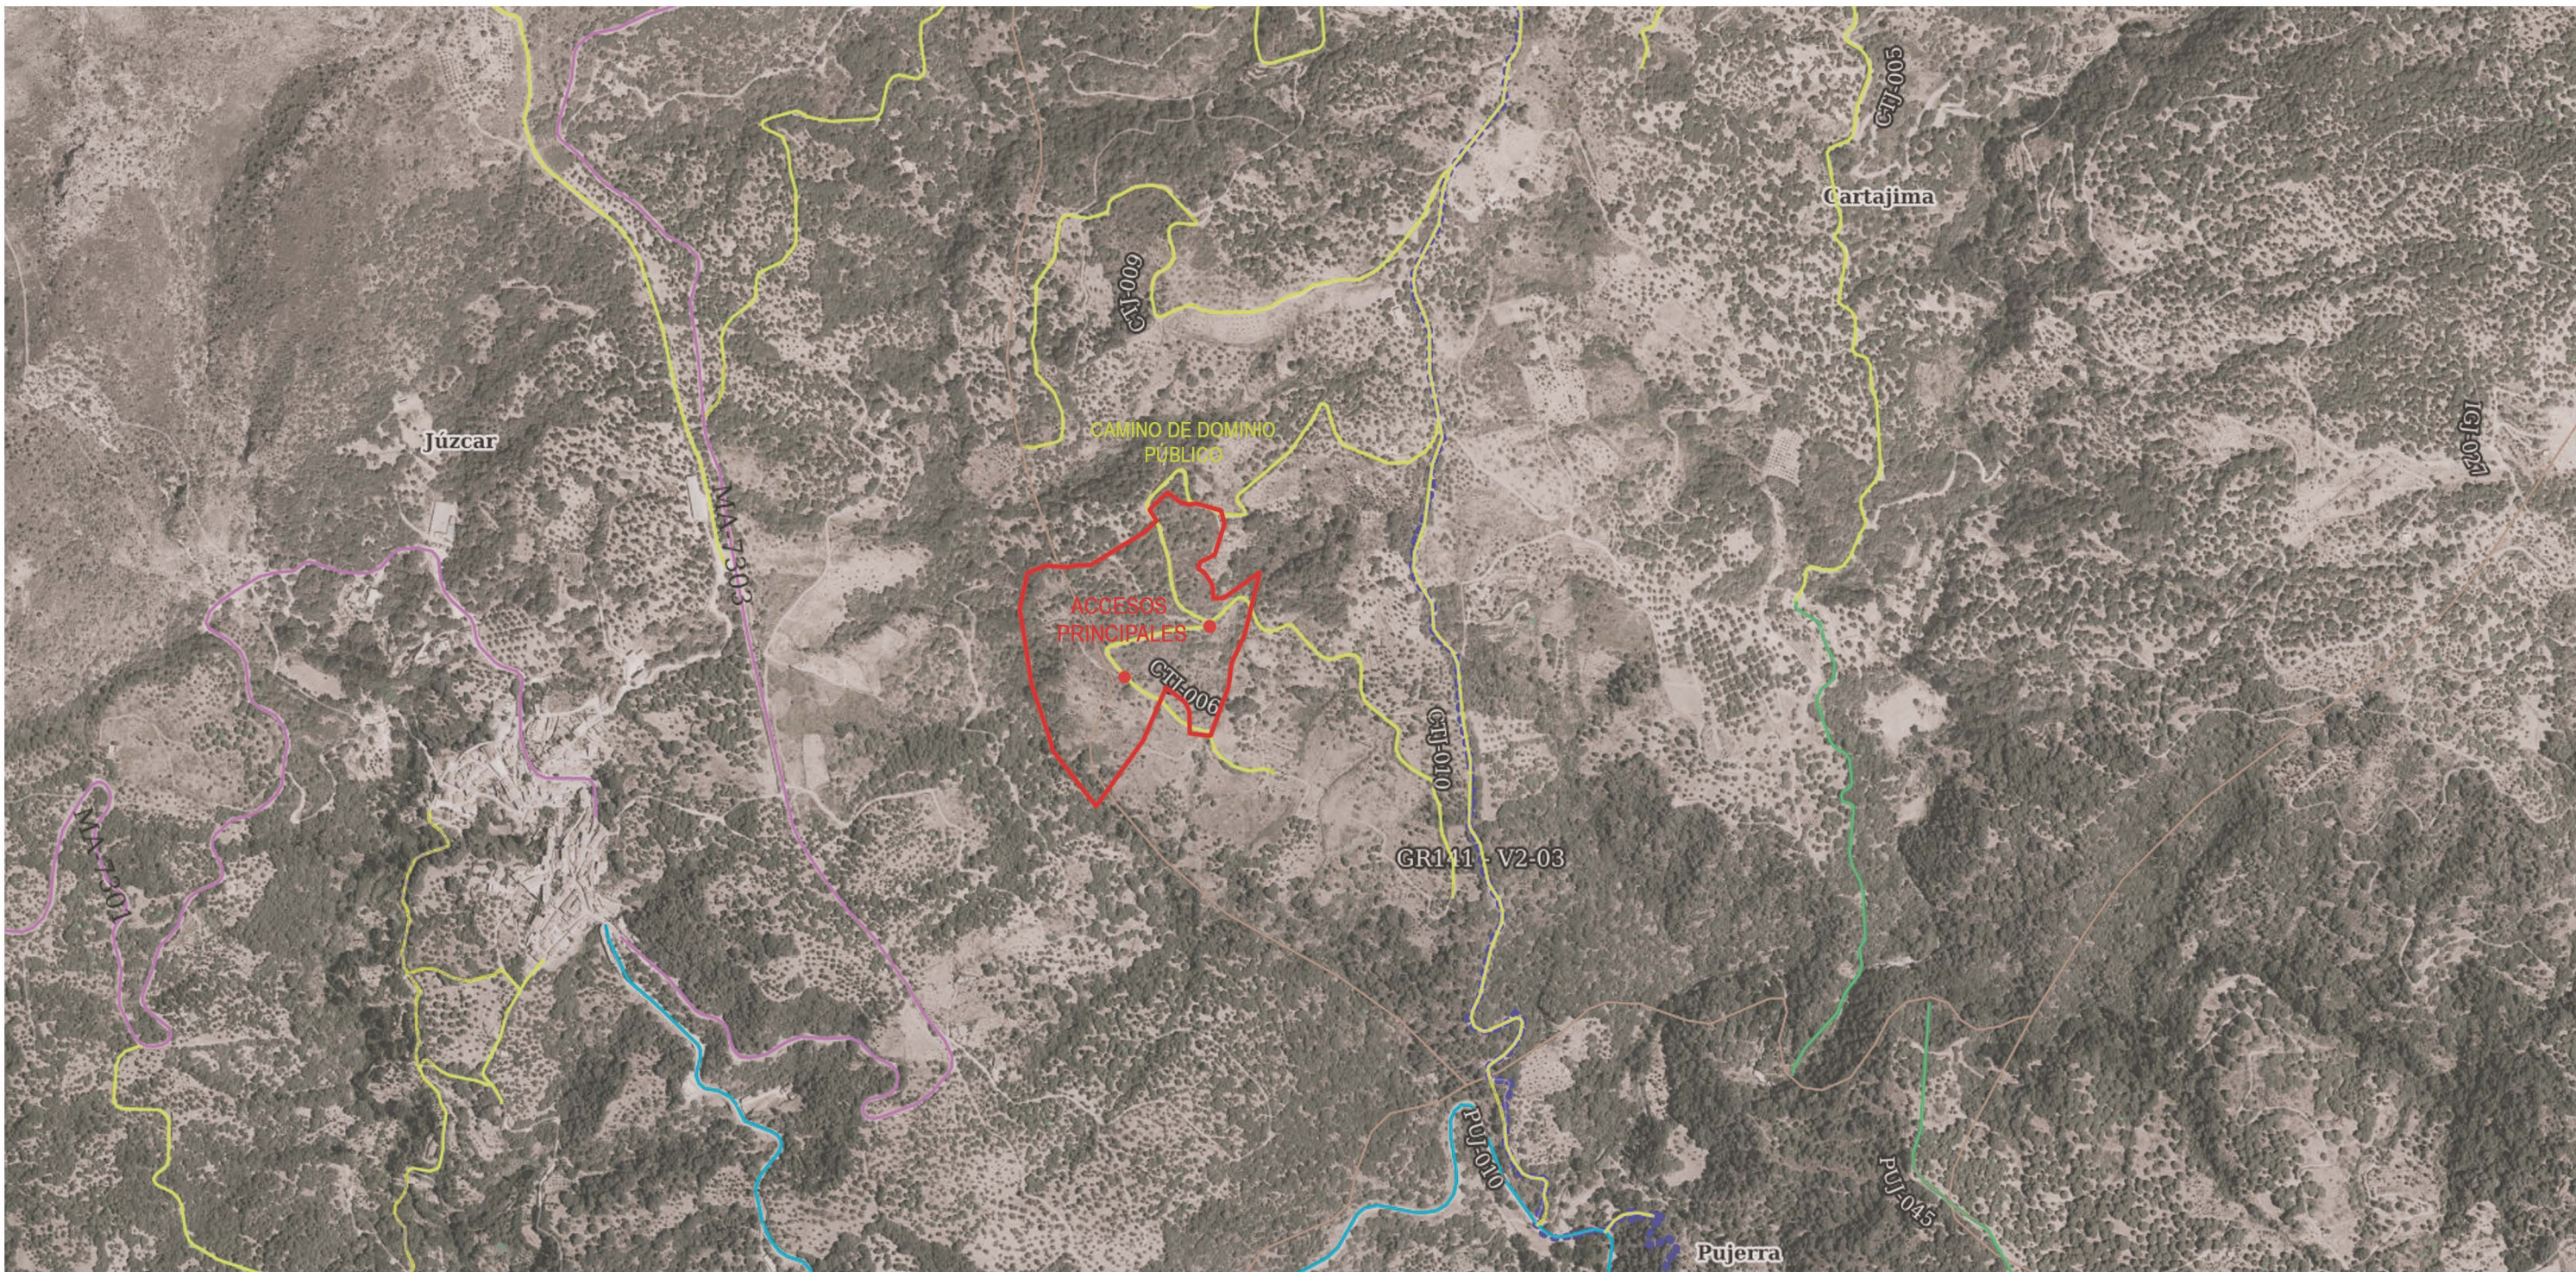




GEORREFERENCIACIÓN		
VIVIENDAS	COORDENADAS X	COORDENADAS Y
1	306740.5756	4055799.2924
2	306768.0434	4055766.5000
3	306802.4197	4055726.2040
4	306763.9811	4055716.5000
5	306797.0827	4055821.9461
6	306815.8738	4055763.0170
7	306687.1652	4055545.6045
8	306753.4668	4055548.0298
9	306778.3367	4055586.3048
10	306655.1918	4055770.3321
ÁREA ESPACIO COMÚN		
A	306730.4616	4055728.7911
B	306752.4272	4055747.7255
C	306728.2696	4055775.7506
D	306706.3039	4055756.8162
EDIFICACIÓN EXISTENTE		
E	306702.9296	4055705.3097
F	306706.0092	4055711.0229
G	306701.5314	4055713.4366
H	306698.4342	4055707.7329
POZO		
CENTRO CIRCUNFERENCIA	306684.1519	4055744.9828

LA GEO-REFERENCIACIÓN DE LAS ECO-VIVIENDAS MARCA EL PUNTO CENTRAL DEL ÁREA CIRCULAR DONDE SE UBICARÁ LA MISMA
SU DISPOSICIÓN EXACTA ESTARÁ EN FUNCIÓN DEL ESTUDIO DEL TERRENO


LOS ACCESOS A LAS ECO-VIVIENDAS SE REALIZARÁN MEDIANTE VEREDADAS DE MÍNIMO IMPACTO DESDE LOS CAMINOS INTERIORES DE PARCELA Y LOS ACCESOS EXTERIORES DEL CAMINO DE DOMINIO PÚBLICO

1 KM DISTANCIA MUNICIPIO MÁS CERCANO (JÚZCAR)
2,2 KM DISTANCIA MUNICIPIO PERTENECIENTE (CARTAJIMA)


- POZO Y MANANTIAL
- ACOMETIDA ABASTECIMIENTO DE AGUA
- DA
- LÍNEA DE MEDÍA TENSIÓN
- SERVIDUMBRE LÍNEA DE MEDIA TENSÓN
- TORRETA LÍNEA DE MEDIA TENSIÓN

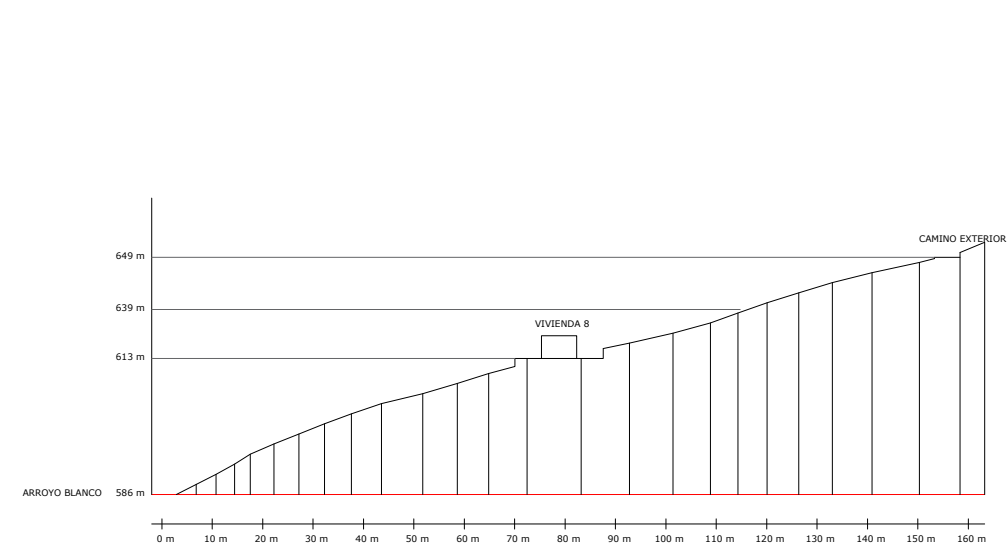


PERFIL DE CORTE 1

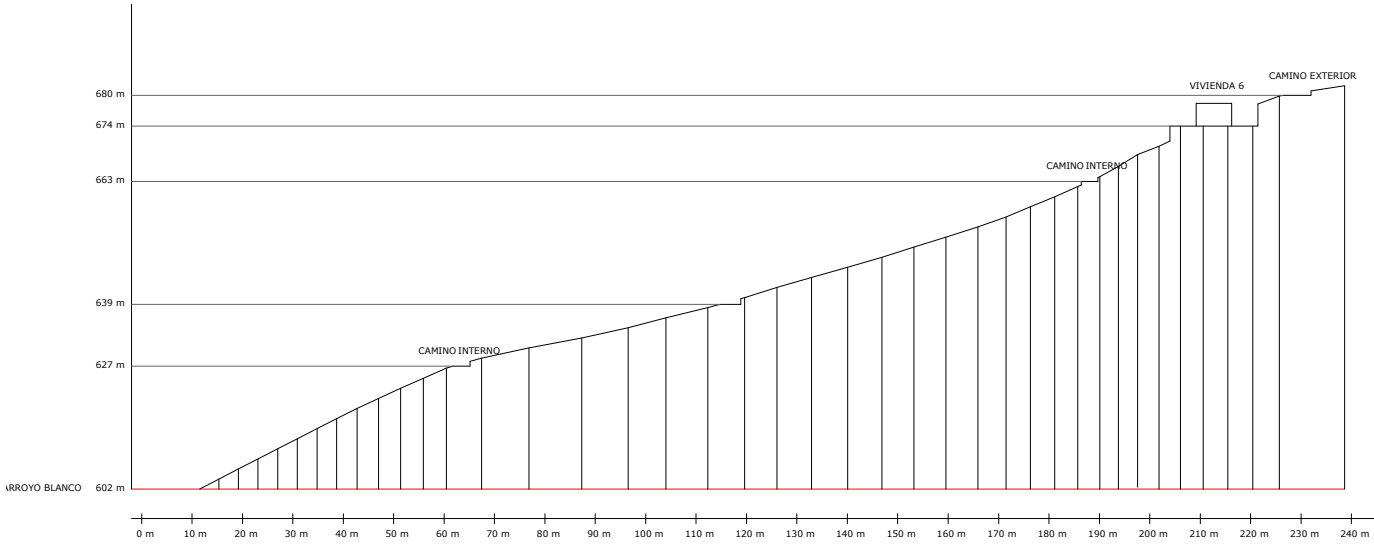


PERFIL DE CORTE 4

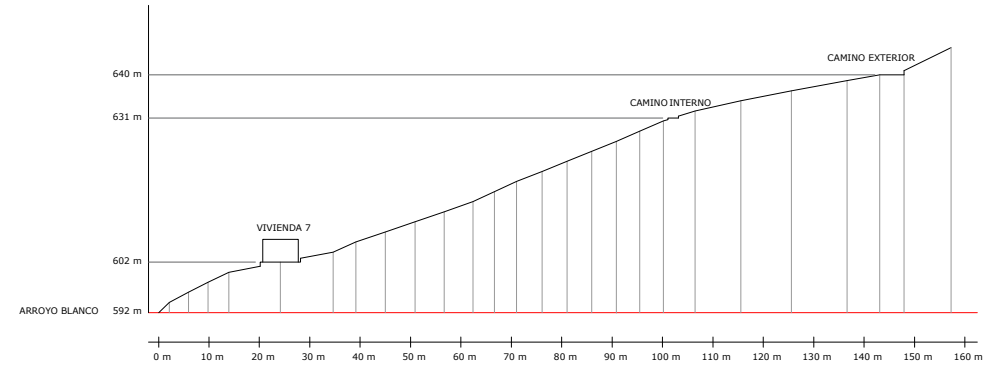


PERFIL DE CORTE 2

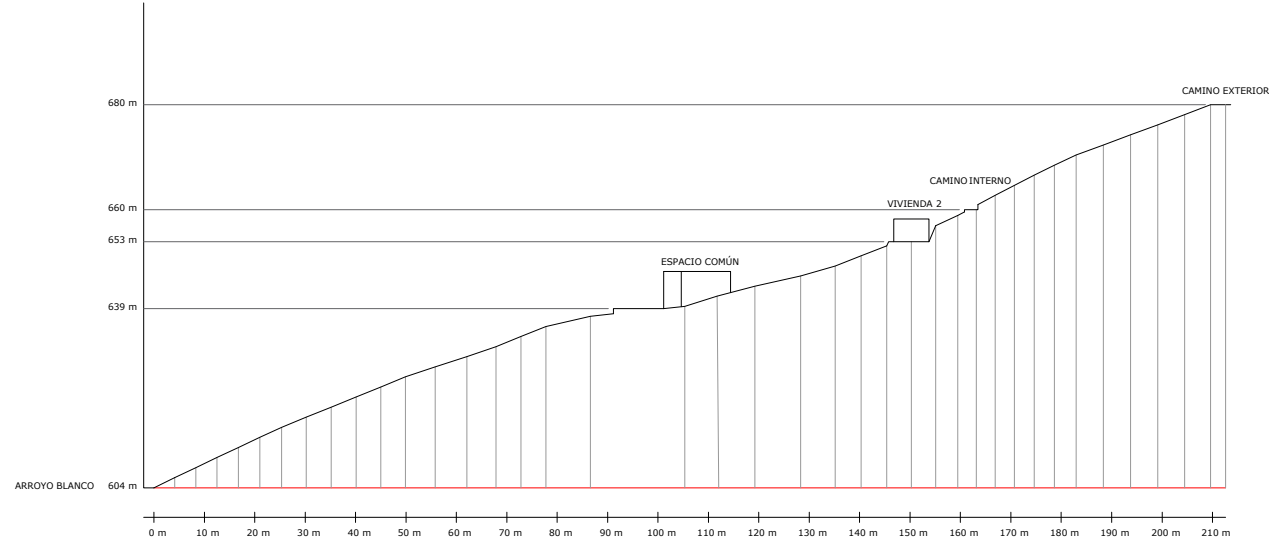

PERFIL DE CORTE 5

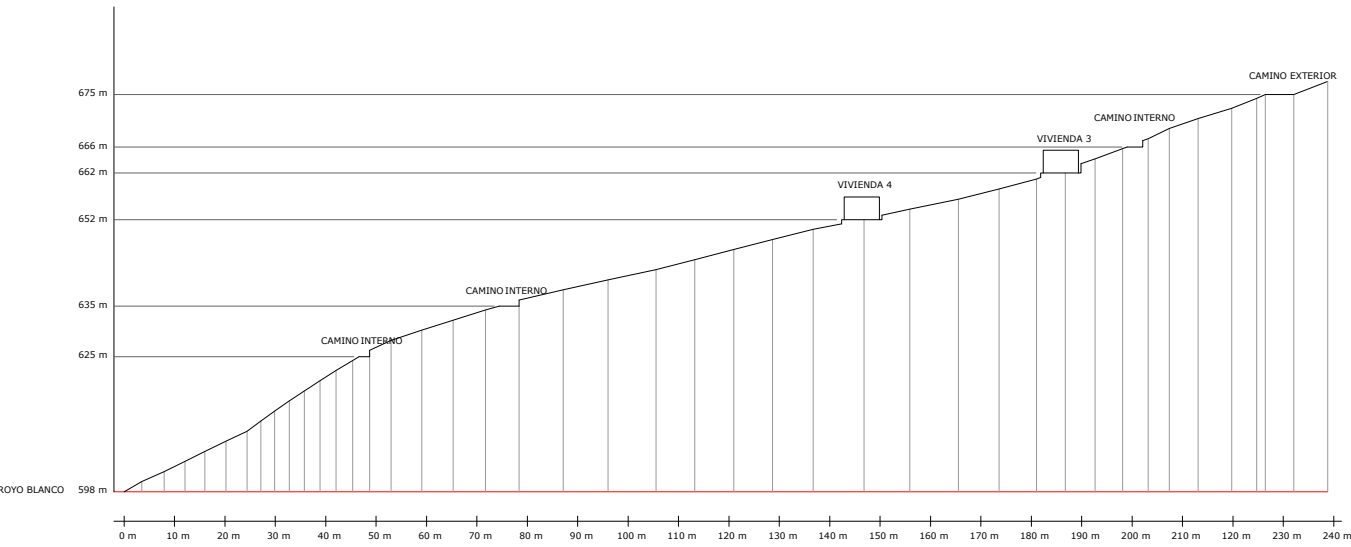

PERFIL DE CORTE 3

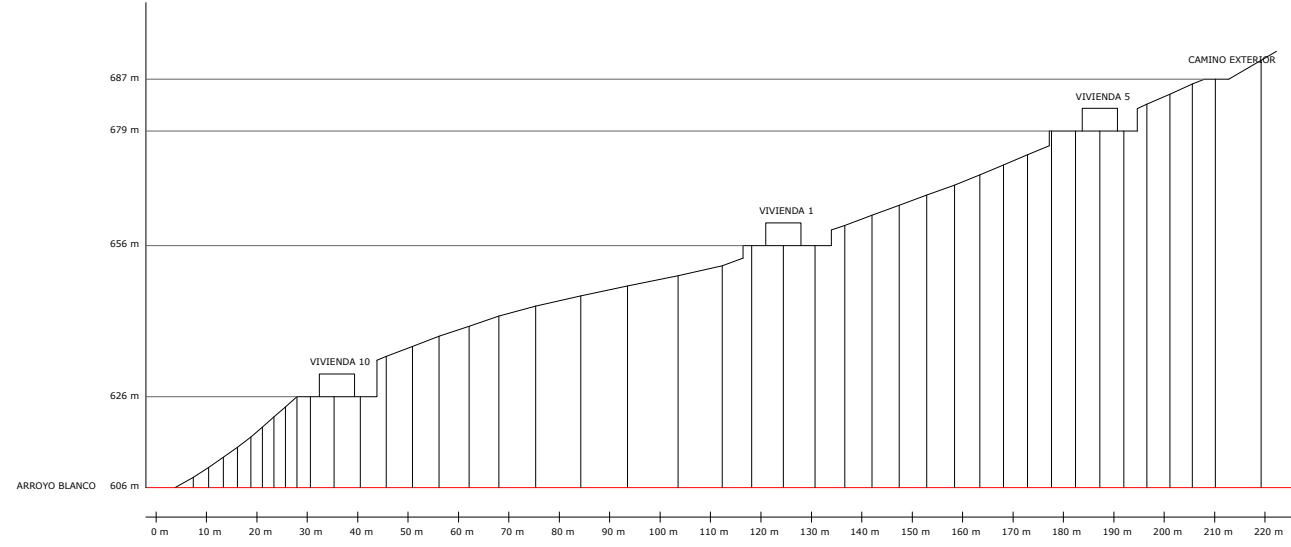


PERFIL DE CORTE 6

PLANO: PERFILES DE CORTE DEL TERRENO CON RESPECTO A LA UBICACIÓN DEL ARROYO_ESCALA 1:1.500


PROYECTO DE ACTUACIÓN CENTRO ECO-TURISMO EN VIÑA DE JUANES, TÉRMINO MUNICIPAL DE CARTAJIMA -MÁLAGA

arquitecto: Rafael Segundo Navarro_colaborador: Miguel Orozco Martín


fecha: 12 de Septiembre de 2025

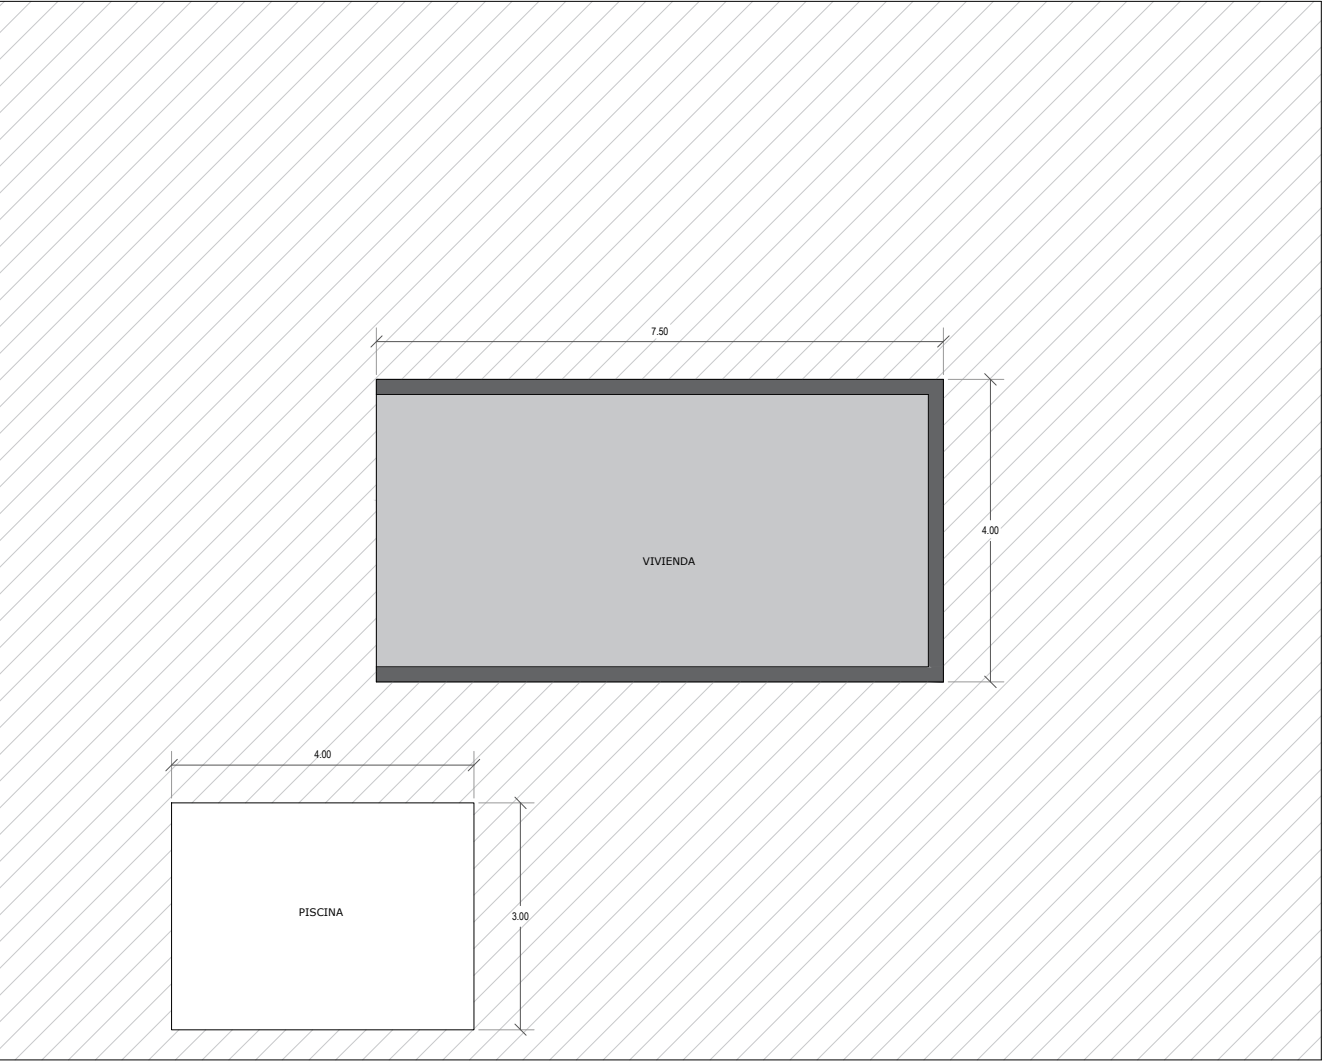


DESARROLLO ESQUEMÁTICO DE LA SUPERFICIE DE UNA UNIDAD DE VIVIENDA Y PISCINA CON SU ÁREA DE INFLUENCIA ESCALA 1:100

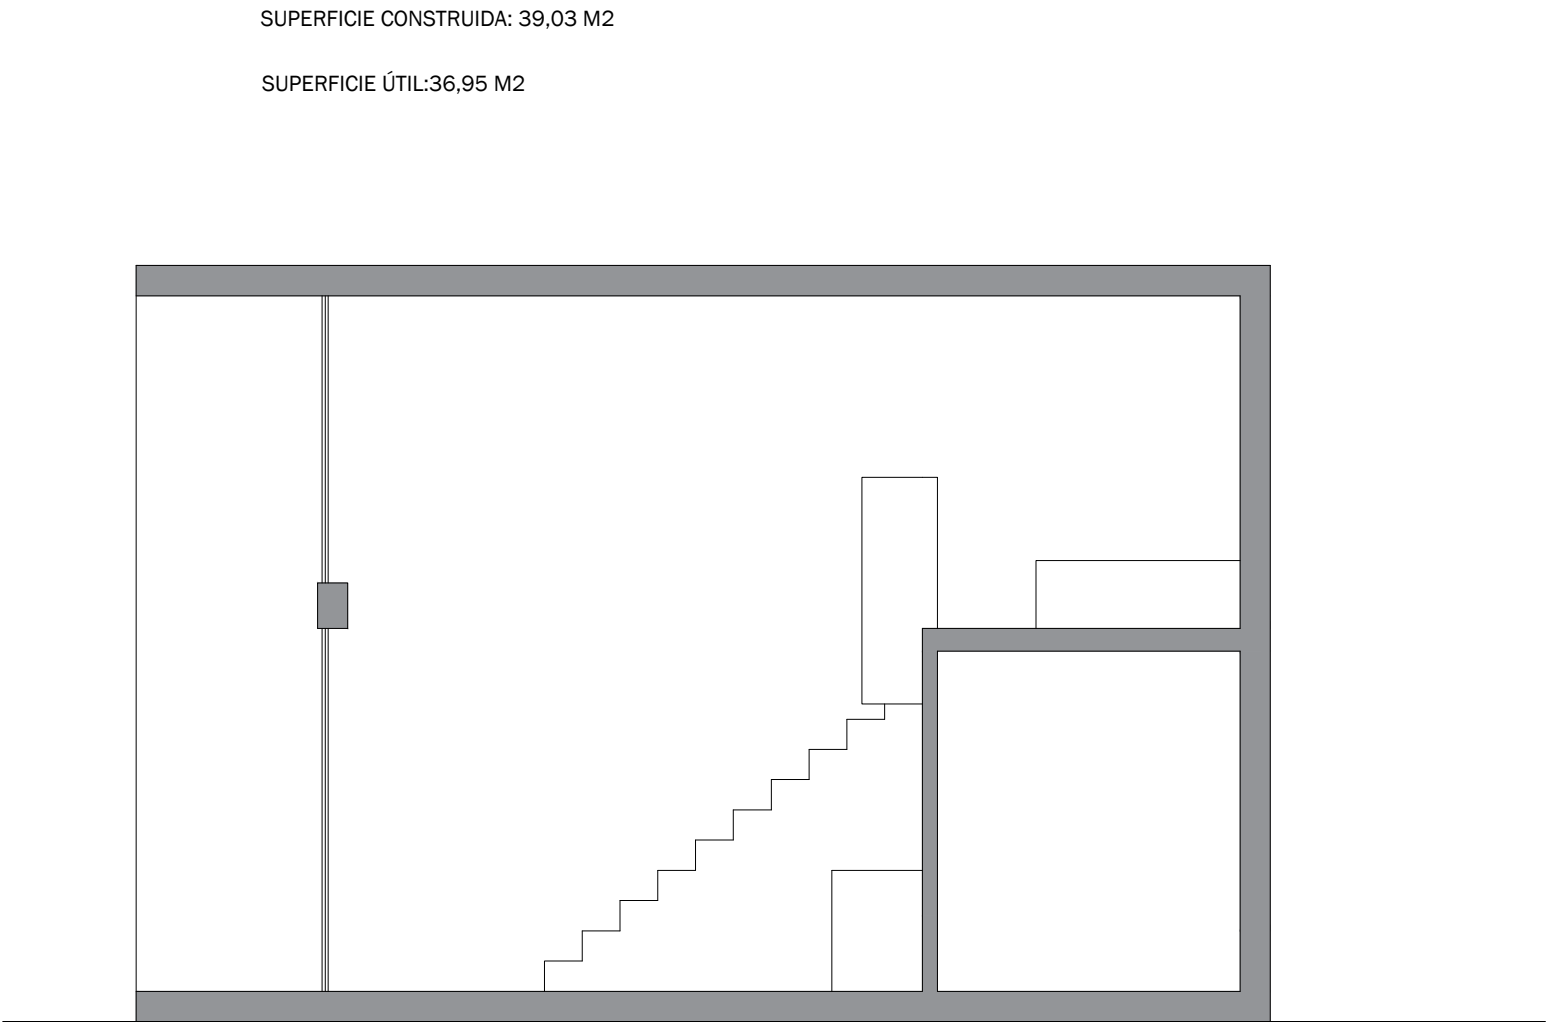


SECCIÓN PROTOTIPO ESCALA 1:50

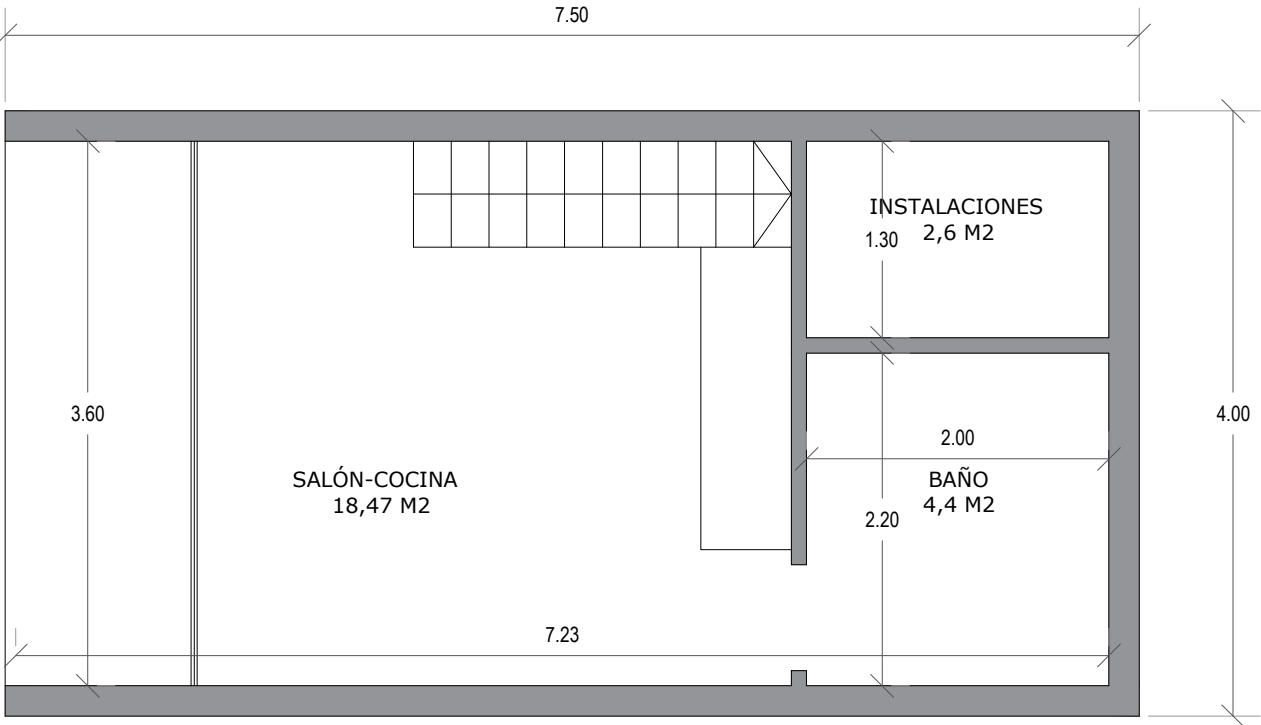

PLANTA BAJA PROTOTIPO ESCALA 1:50

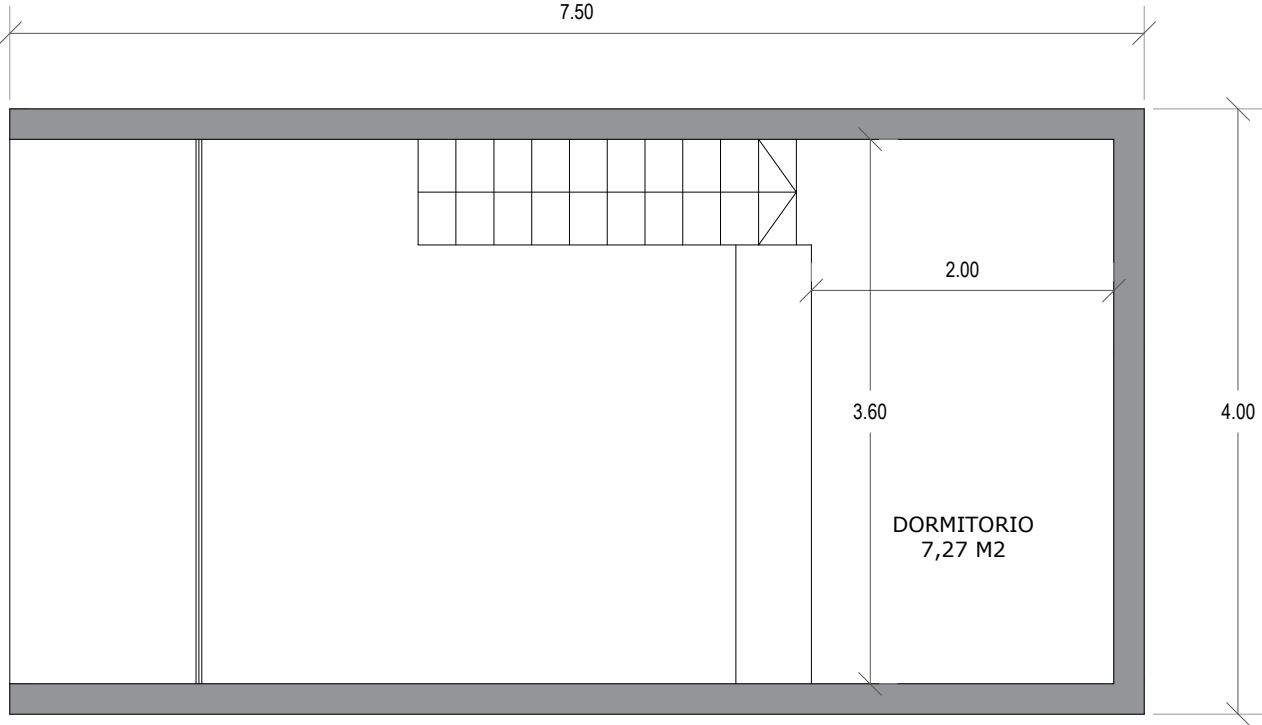


PLANTA ALTA PROTOTIPO ESCALA 1:50

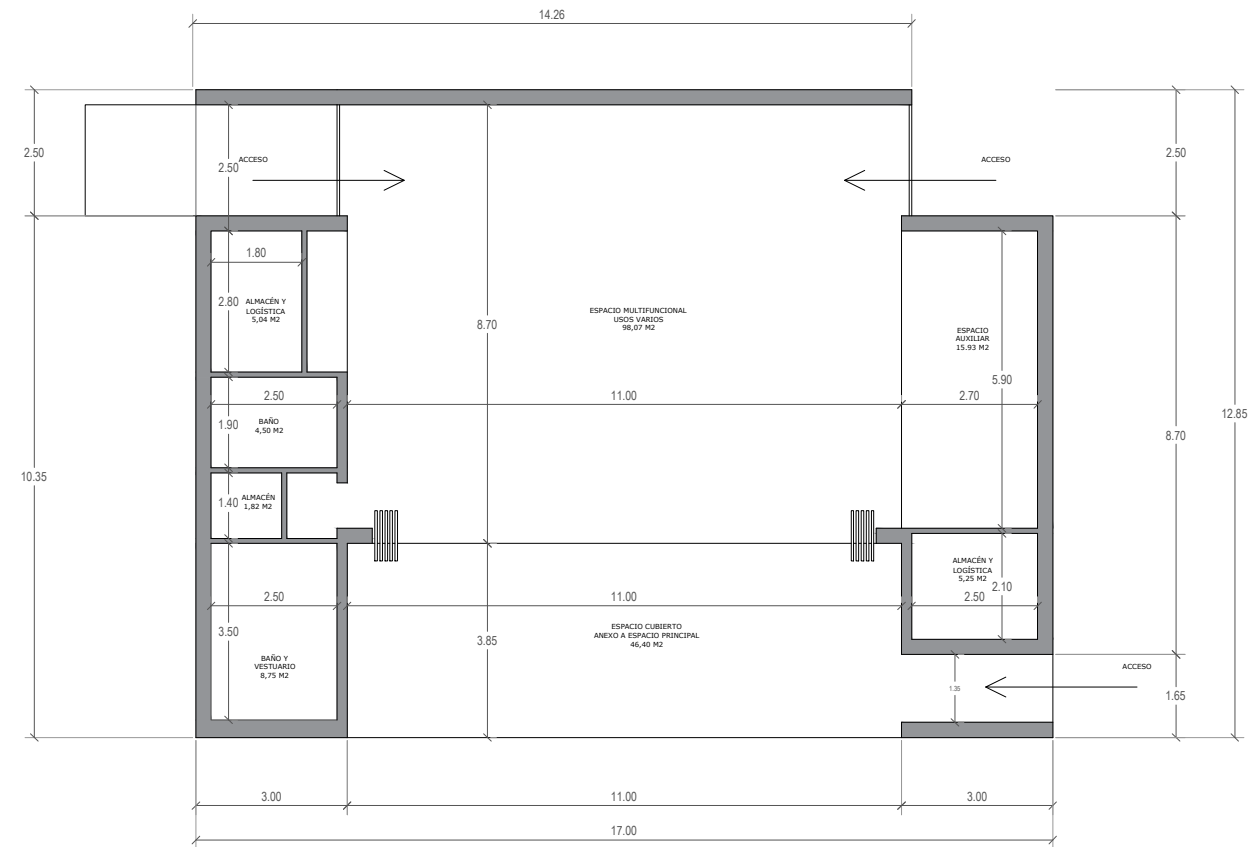


SUPERFICIE CONSTRUIDA: 211,45 M2

SUPERFICIE ÚTIL:162,56 M2

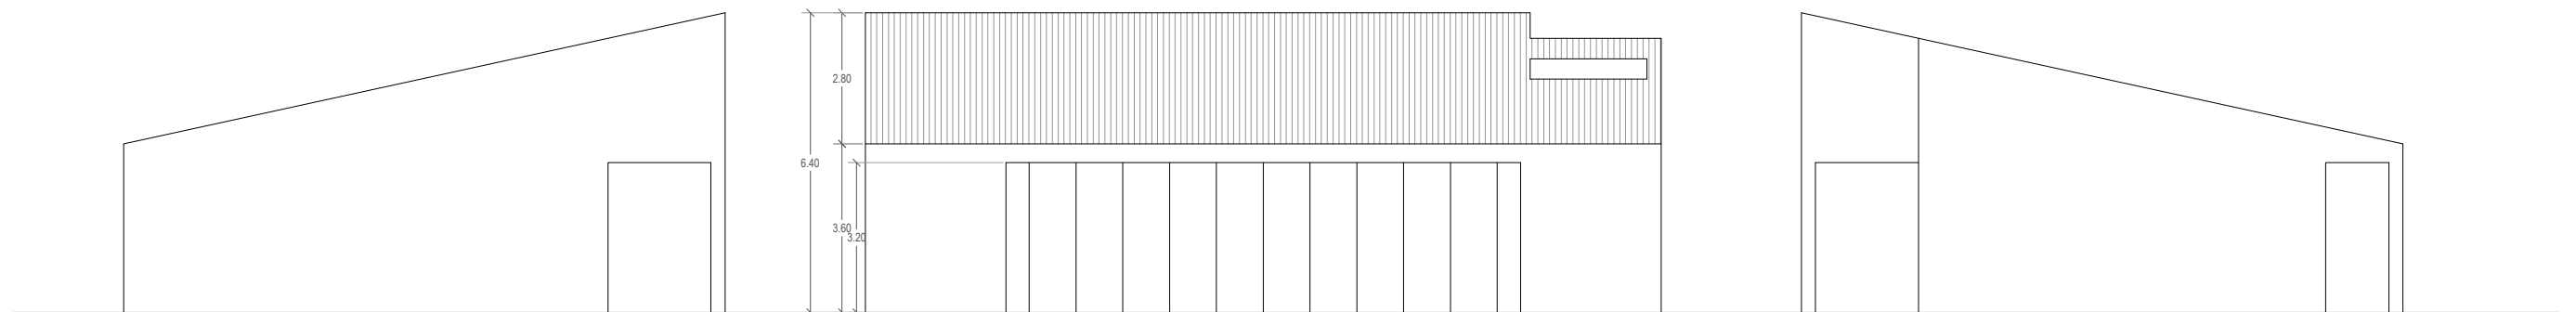


POSIBLE PROPUESTA DE ESPACIO COMÚN PLANTA MODELO UTILIZANDO UNA DE LAS CONFIGURACIONES Y SU POSIBLE ALZADO ESCALA 1:150



DIRECCIÓN DE LOS DRENAJES DEL TERRENO

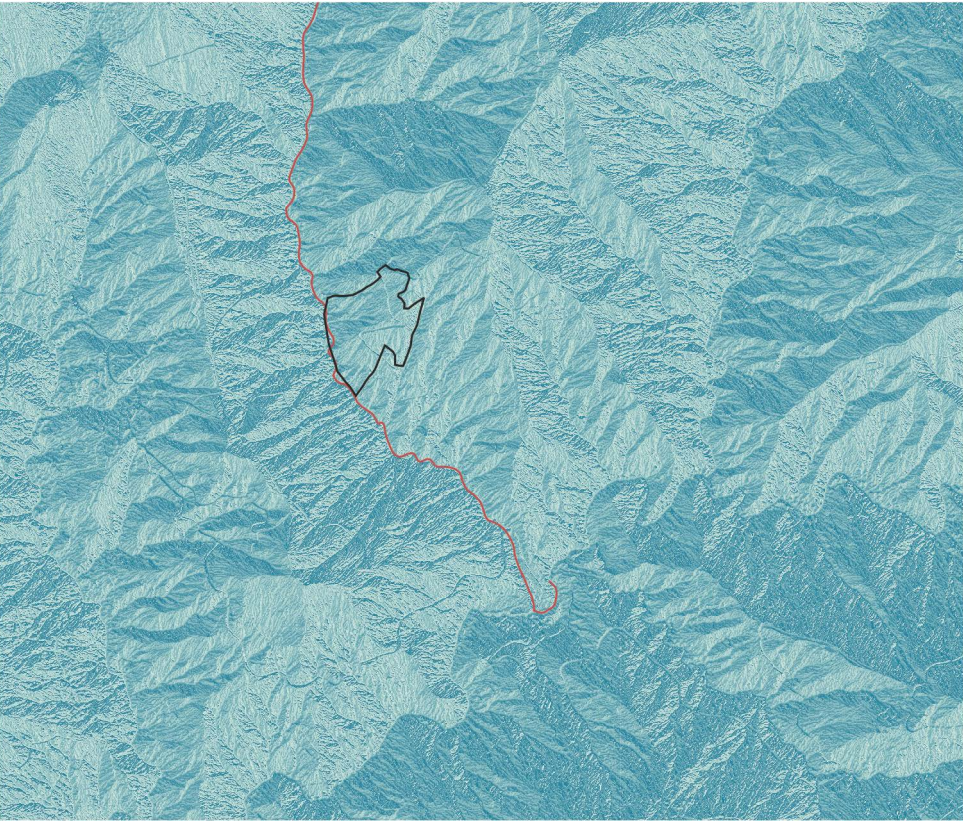

TOPOGRÁFICO Y PENDIENTES DEL TERRITORIO


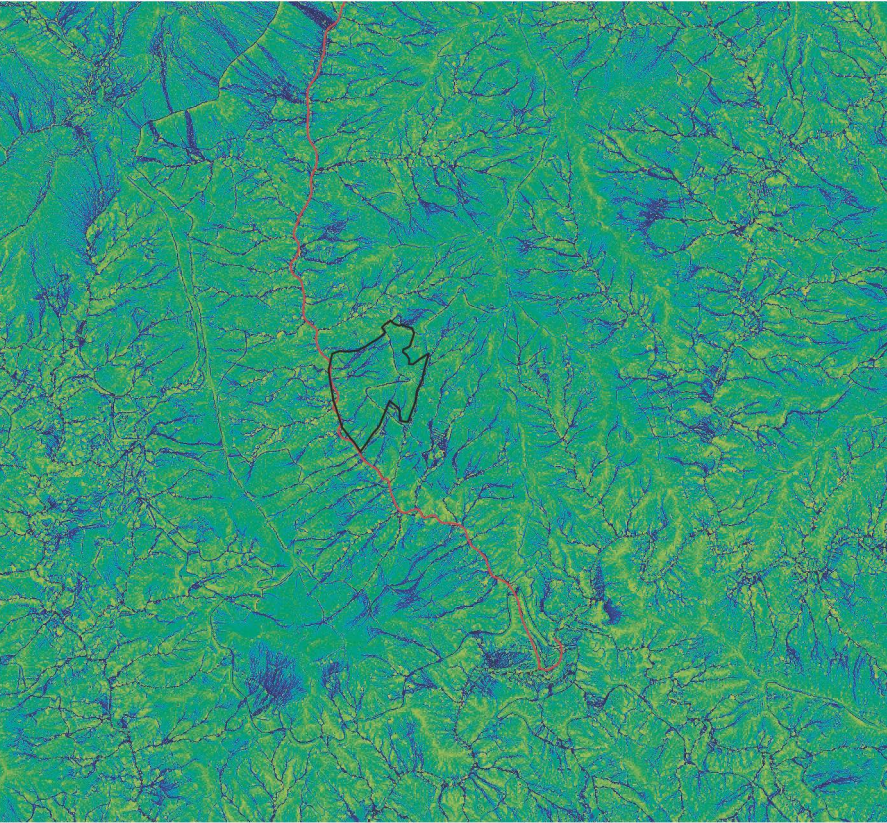


AFLUENTES Y CUENCAS ARROYO BLANCO

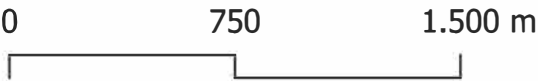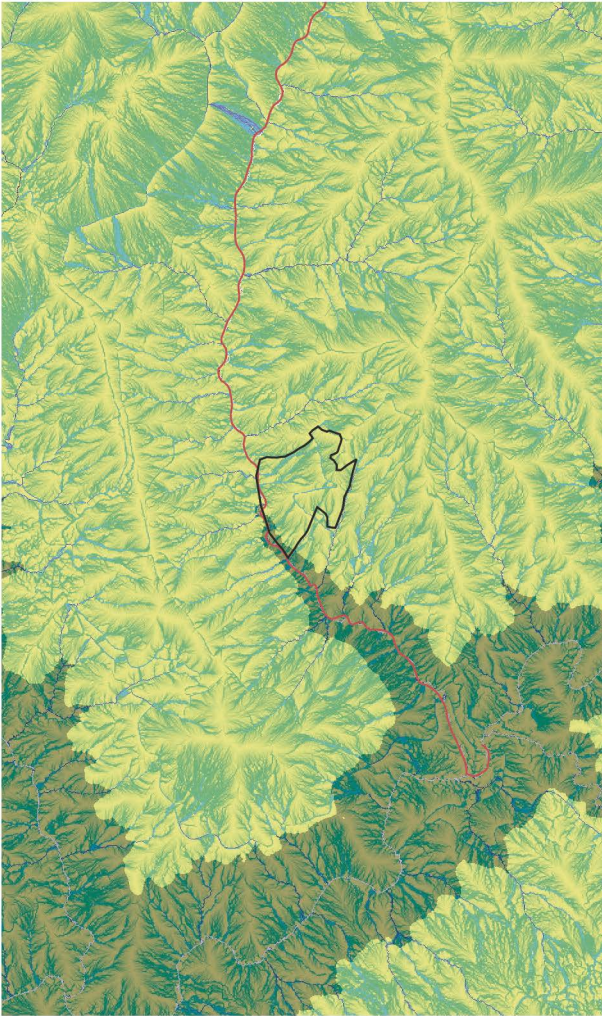

*EN LÍNEA ROJA SE RECOGE EL CURSO DEL 'ARROYO BLANCO' OBJETO DE ESTUDIO HIDROGRÁFICO Y QUE MARCA EL LÍMITE INFERIOR DE LA PARCELA

PLANO AFLUENTES PRINCIPALES Y CONEXIÓN CON EL RÍO GENAL

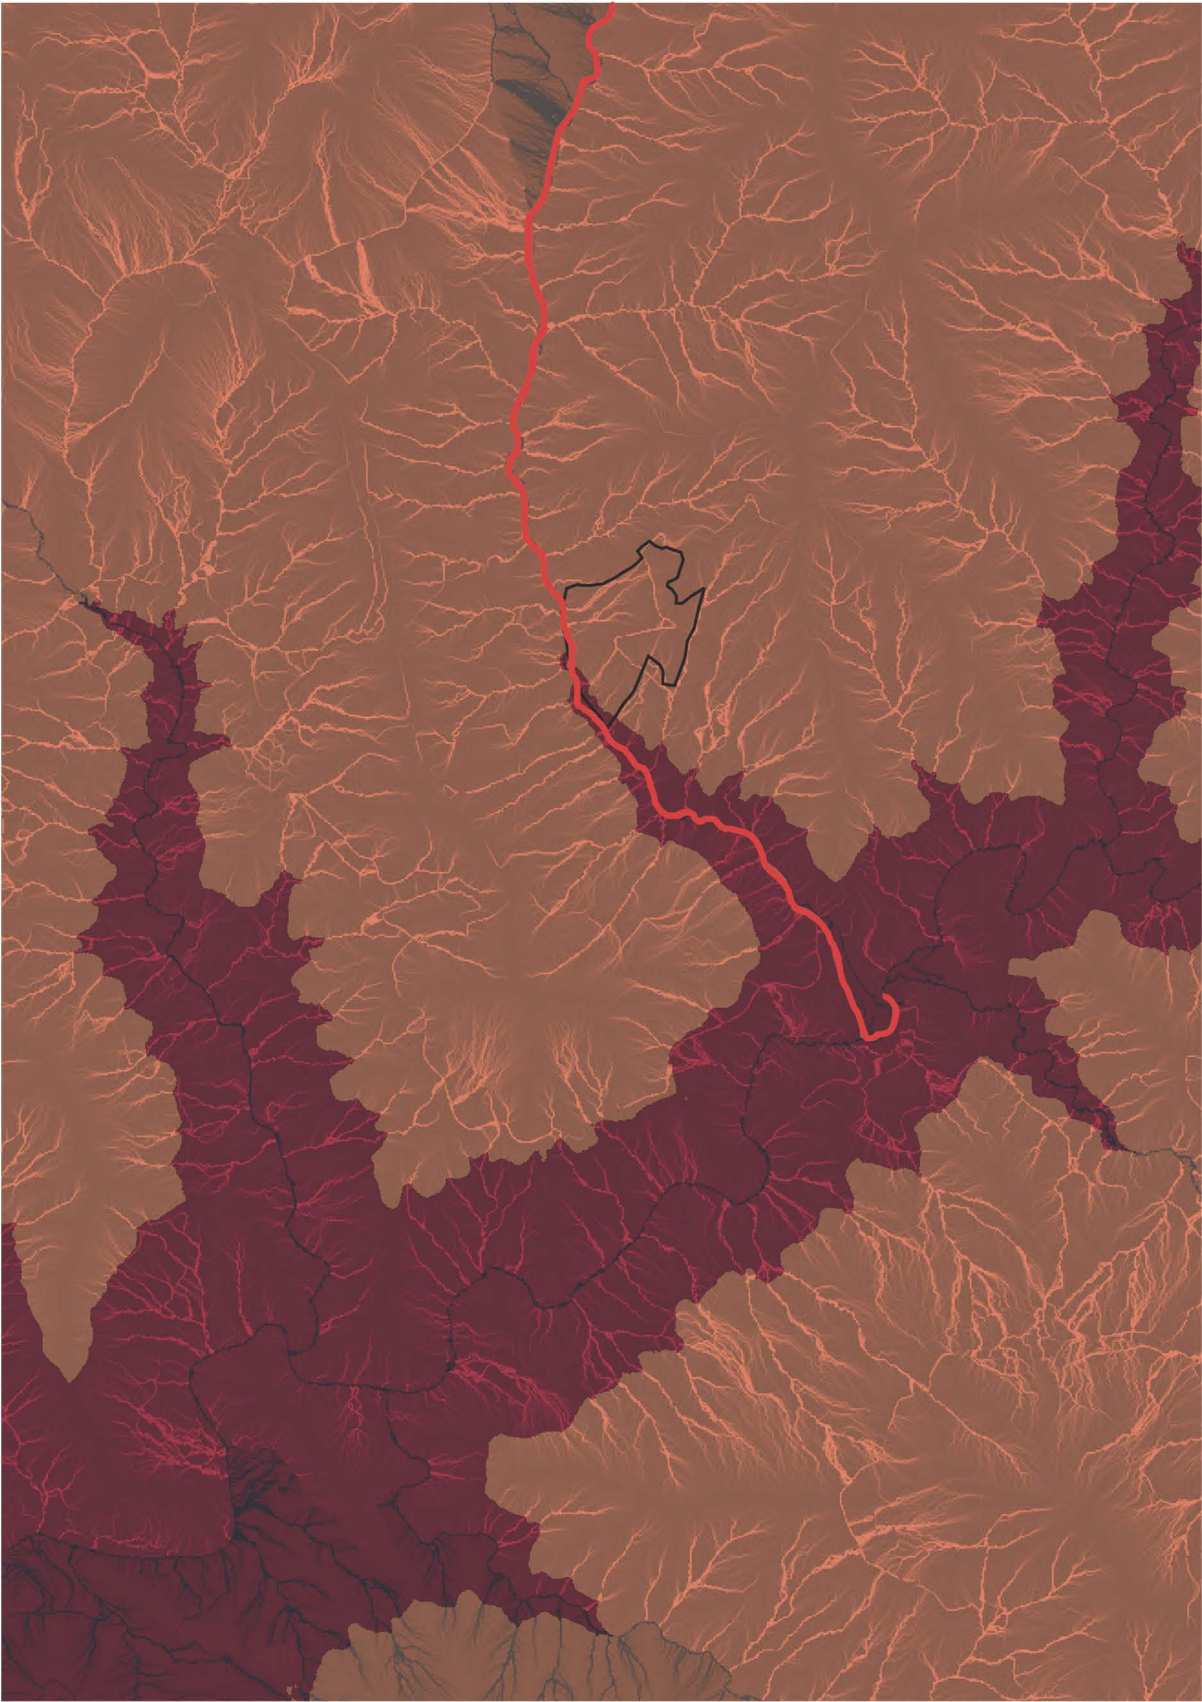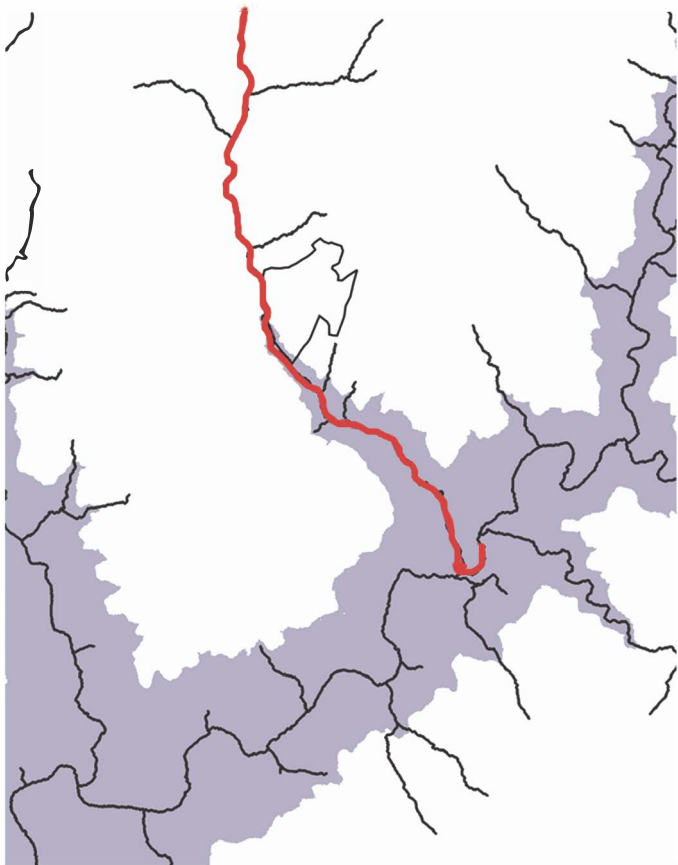

PLANO DE CURSOS Y ZONA INUNDABLE DEL ARROYO Y RÍO GENAL

LOS PLANOS RECOGEN LA POSIBLE ZONA DE AFECCIÓN POR INUNDACIÓN DEL RIO GENAL Y SUS AFLUENTES Y ARROYOS MÁS IMPORTANTES.

ENTRE ELLOS, EN ROJO, EL ARROYO BLANCO, QUE DELIMITA NUESTRA PARCELA.

ESTA SIMULACIÓN DE INUNDACIÓN ESTÁ CALCULADA ESTIMATIVAMENTE TAL Y COMO VIENE RECOGIDA EN EL ESTUDIO HIDROGRÁFICO DE LA MEMORIA DE ESTE PROYECTO DE ACTUACIÓN.

SE HA TOMADO UNA SITUACIÓN PRÁCTICAMENTE CATASTRÓFICA EN LA QUE LA COTA DE INUNDACIÓN LLEGARA A LOS 596M Y CALCULANDO QUE LAS CUENCAS TUVIESEN UNA PROFUNDIDAD DE 0.5M DEBIDO A MAL ESTADO, FORRAJE Y OBSTÁCULOS Y PARA UN PERIODO DE RETORNO DE 500 AÑOS.

AÚN ESTABLECIENDO ESTA SITUACIÓN TAN EXCESIVA Y POCO PROBABLE, LA PARCELA APENAS SE VERÍA AFECTADA Y LAS COTAS INUNDABLES NO AFECTARÍAN A NINGUNA DE LAS UBICACIONES DE LOS EDIFICIOS.

EL EL PLANO Nº8 SE RECOGEN LOS PERFILES DE CORTE DEL TERRENO Y SE APRECIA QUE TODAS LAS CONSTRUCCIONES ESTÁN SITUADAS POR ENCIMA DE LA COTA DE 596M.



IMÁGENES DE LA PARCELA Y EL ENTORNO



INFOGRAFÍAS DE ESTUDIO DE LA ECO VIVIENDA Y EL ESPACIO COMÚN